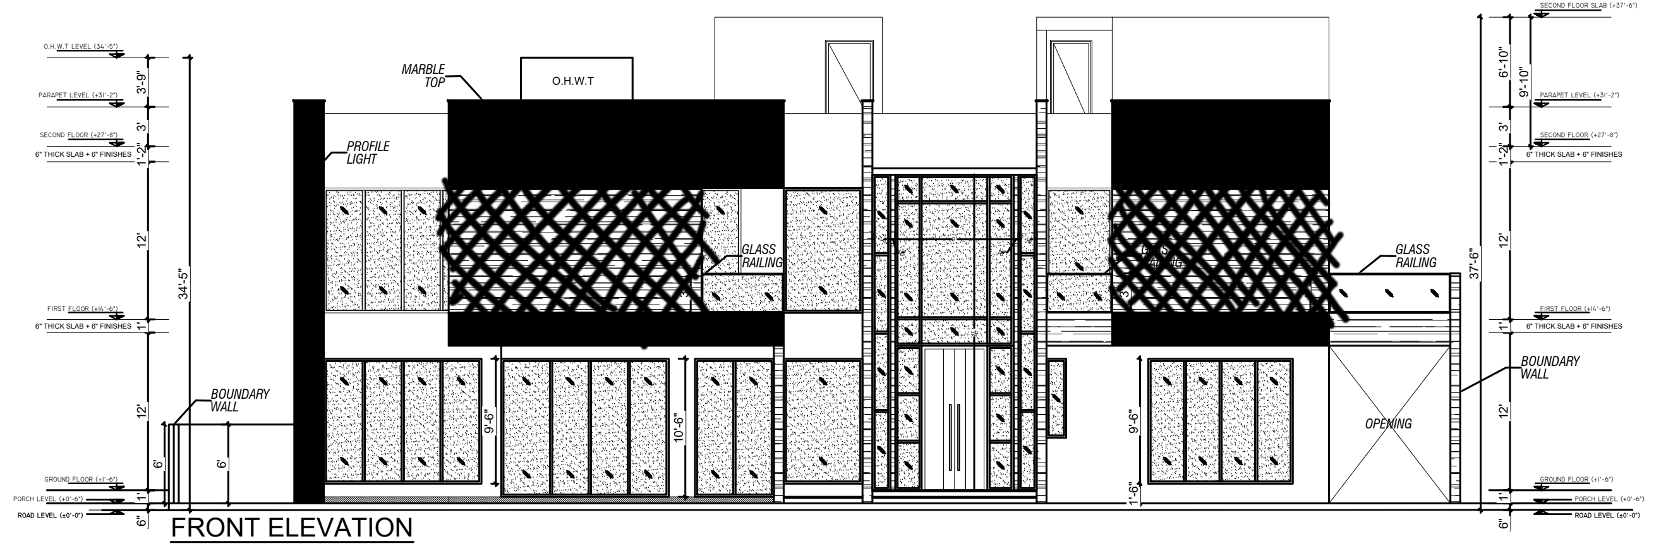

FRONT ELEVATION

SCALE = 1/8"=1'-0"

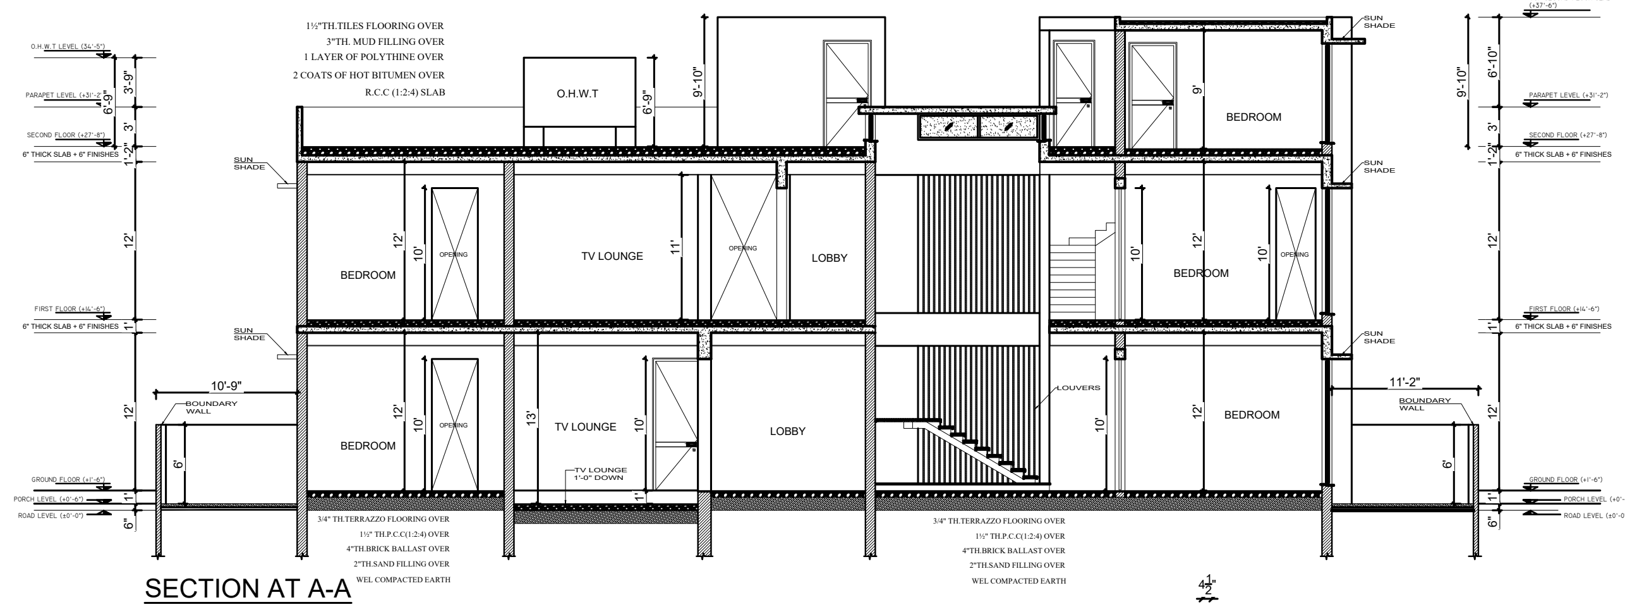

SECTION AT A-A

SCALE = 1/8"=1'-0"

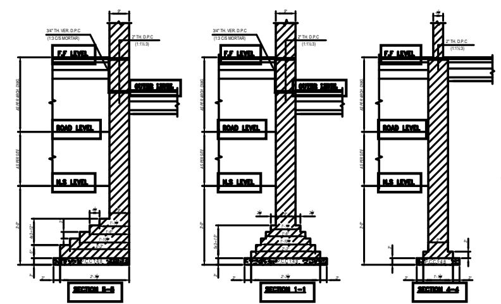

FOUNDATION DETAIL

SCALE= 1/4"=1'-0"
AS PER STR. DWGS

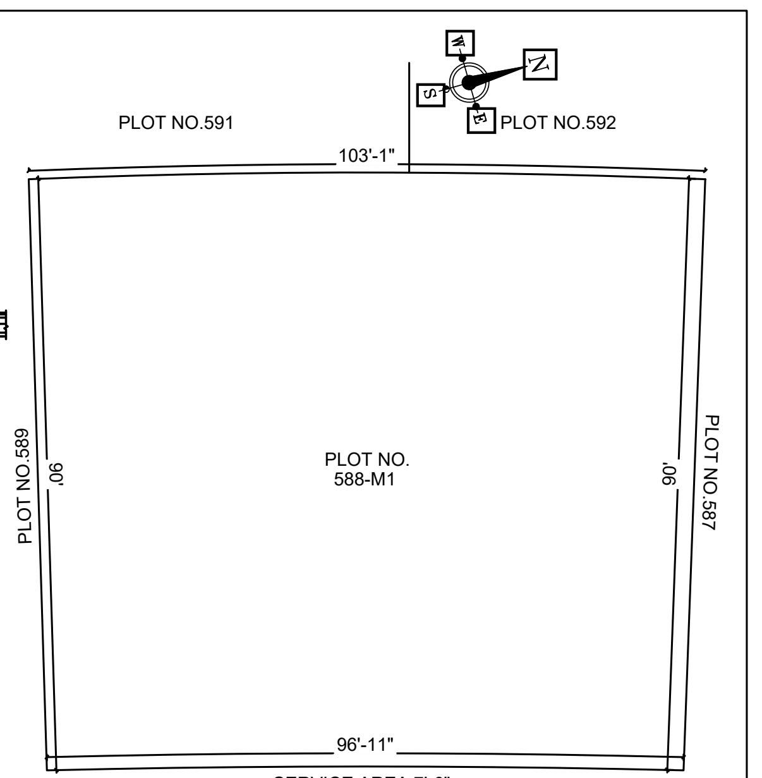

SITE PLAN

SCALE = 1/16"=1'-0"

SERVICE AREA 7'-6"

ROAD 35'-0" WIDE

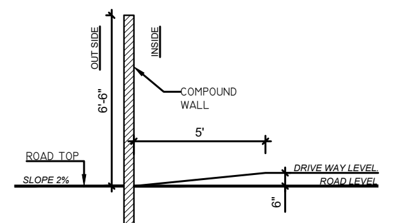

BOUNDARY WALL & RAMP DETAIL

SCALE = 1/4" = 1'-0"

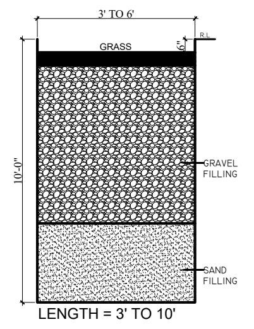

RECHARGE PIT

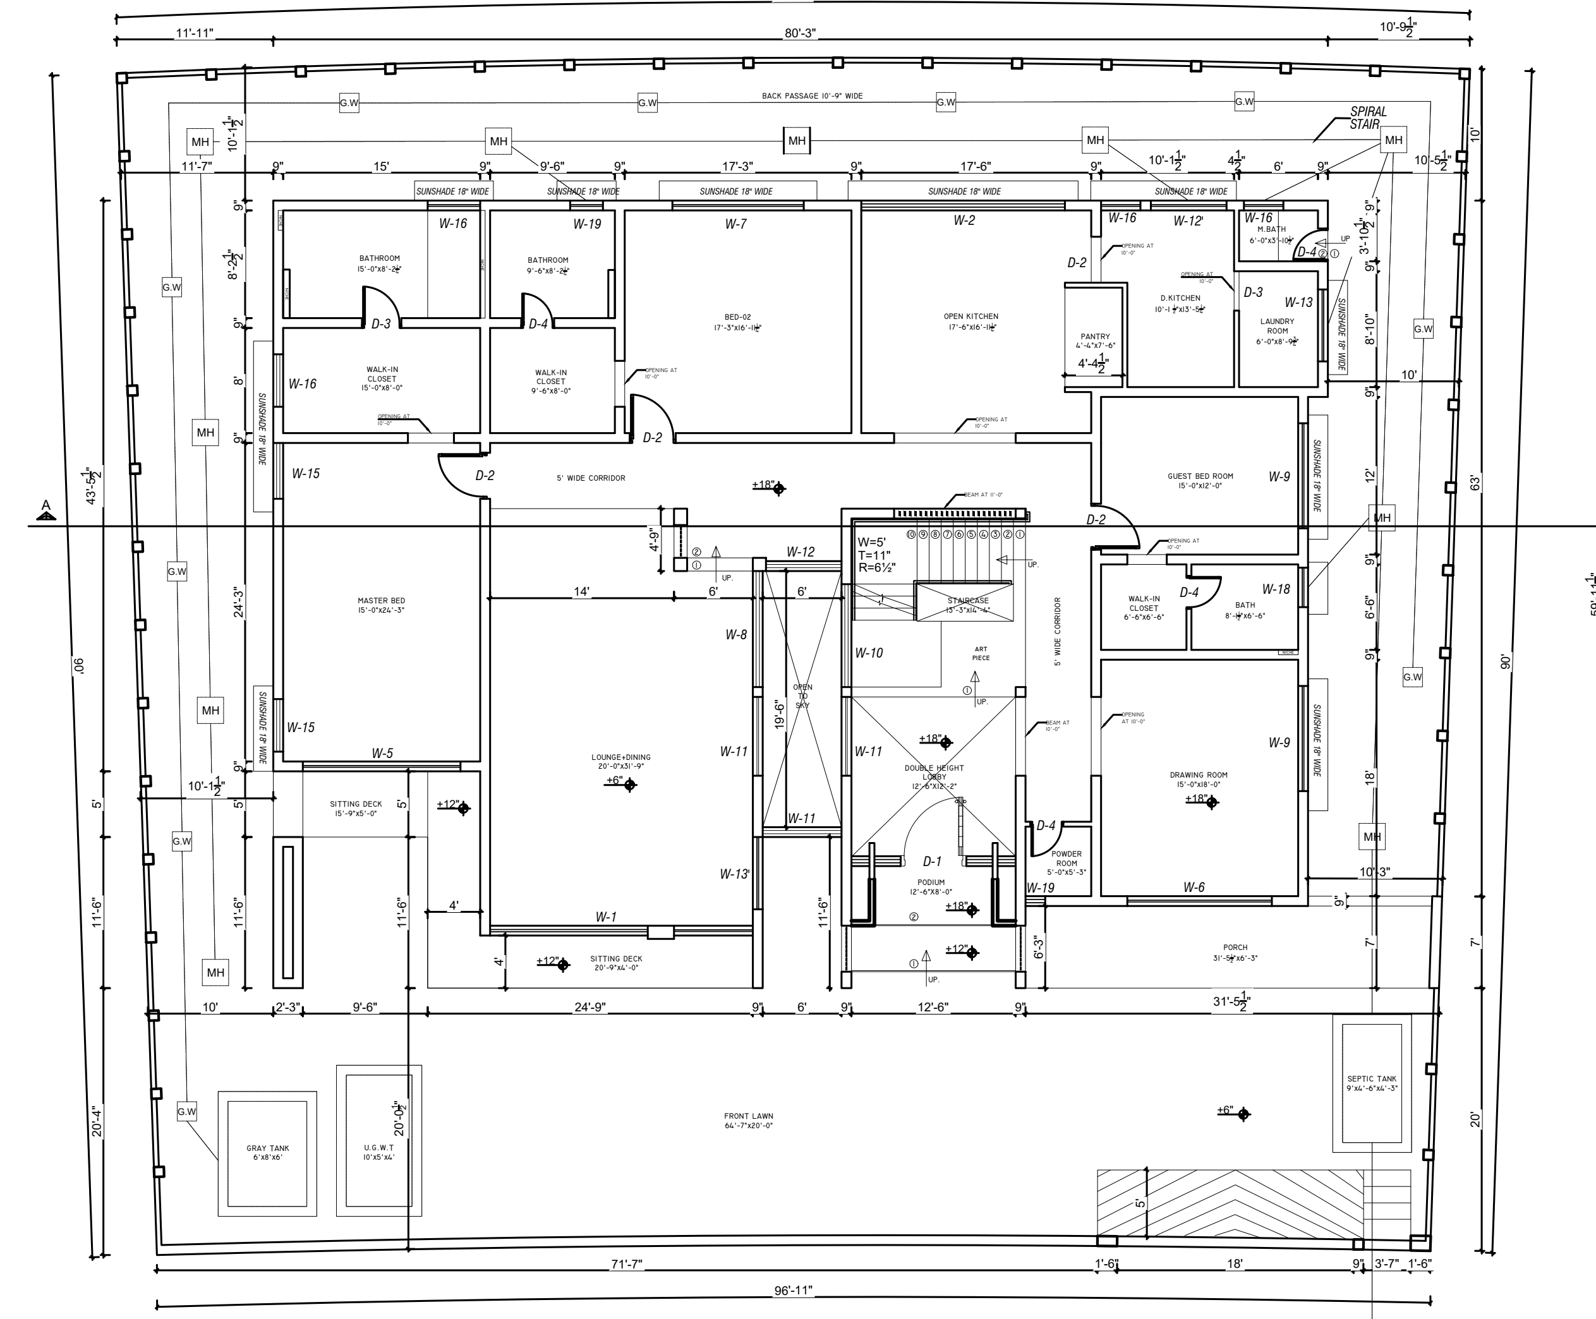

GROUND FLOOR PLAN

SCALE = 1/8"=1'-0"

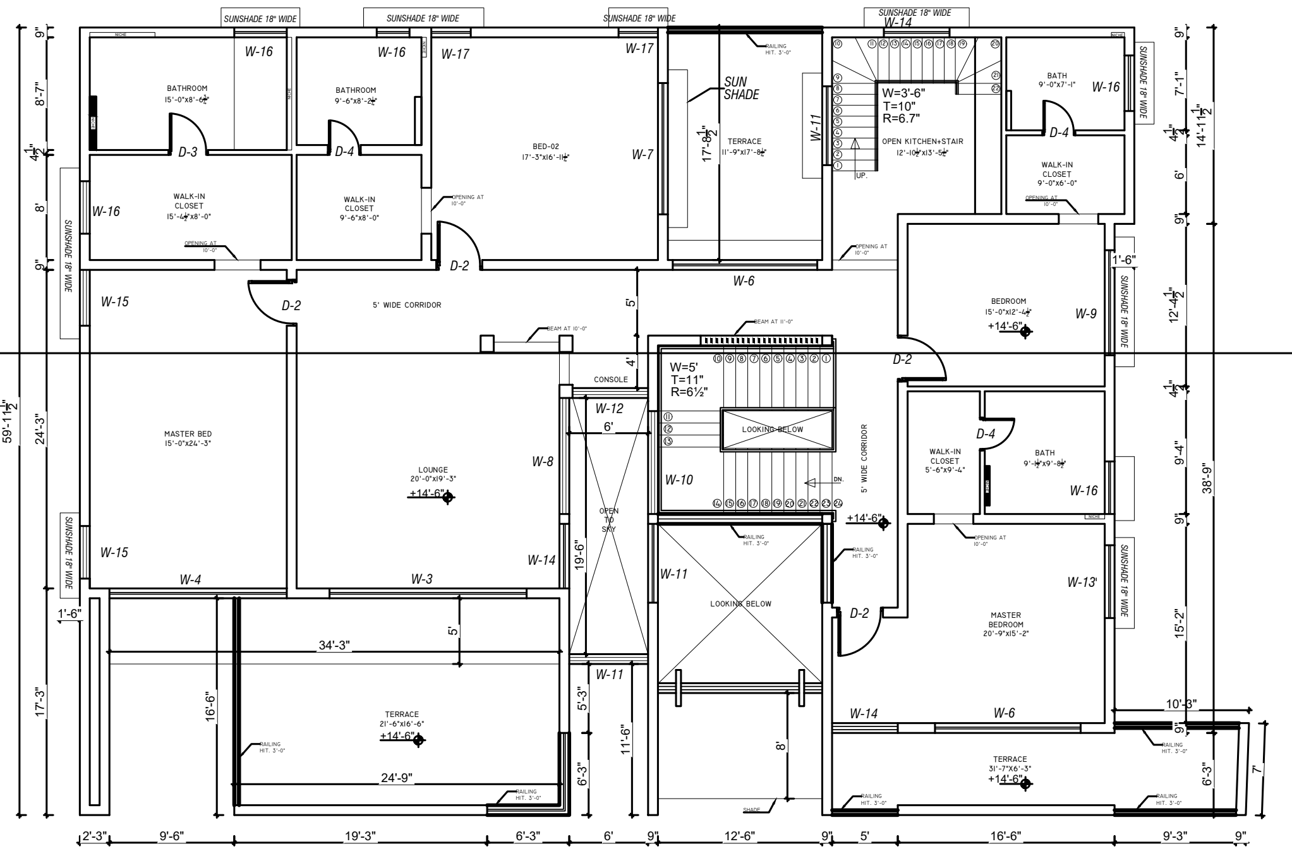

FIRST FLOOR PLAN

SCALE = 1/8"=1'-0"

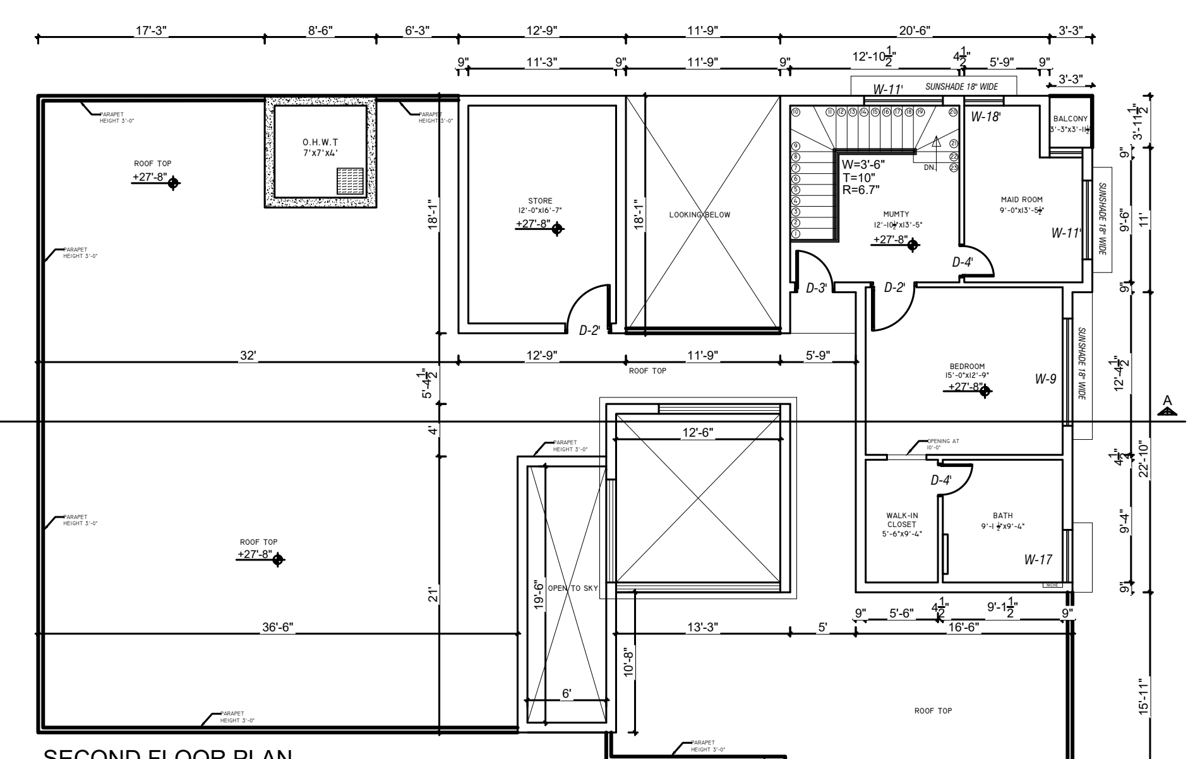

SECOND FLOOR PLAN

SCALE = 1/8"=1'-0"

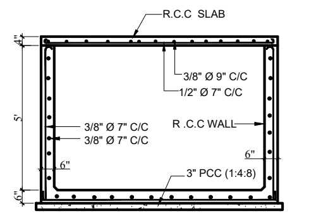

U.G WATER TANK

SCALE : 1/4" = 1'-0"

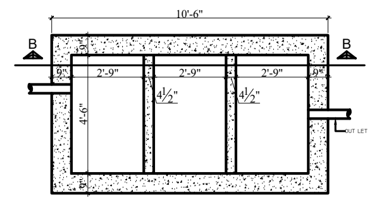

PLAN SEPTIC TANK

SCALE : 1/4" = 1'-0"

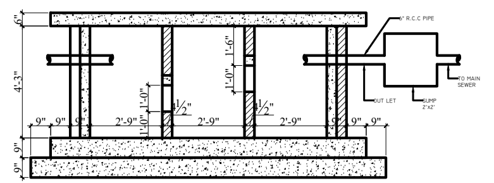

SECTION AT B-B

SCALE : 1/4" = 1'-0"

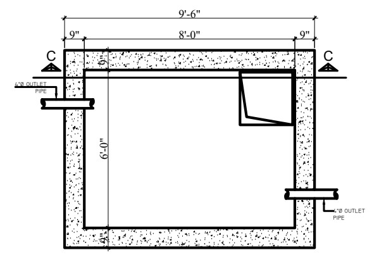

PLAN GRAY TANK

SCALE : 1/4" = 1'-0"

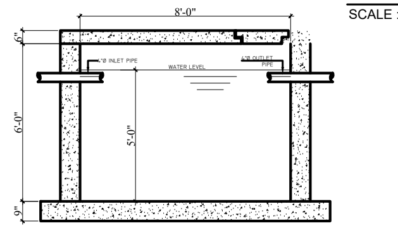

SECTION AT C-C

SCALE : 1/4" = 1'-0"

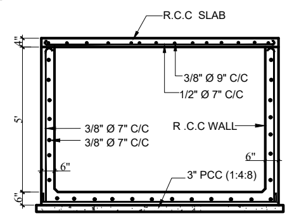

RAIN WATER TANK

SCALE : 1/4" = 1'-0"

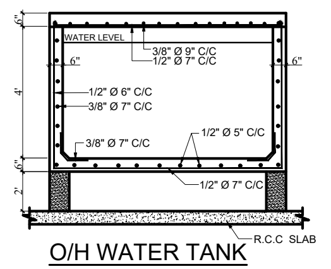

O/H WATER TANK

SCALE : 1/4" = 1'-0"

AREA STATEMENT

TITLE	AREA
TOTAL PLOT AREA	9000 SFT.
GROUND FLOOR COVERED AREA	4,435 SFT.
FIRST FLOOR COVERED AREA	3,670 SFT.
SECOND FLOOR COVERED AREA	980 SFT.
TOTAL COVERED AREA	9,085 SFT.
OPEN AREA OF PLOT	4,565 SFT.

SCHEDULE OF D/WINDOWS.

TYPE	SIZE	SILL	DESCRIPTION
D-1	5'-0"x24'-0"	0'-0"	SOLID WOOD+GLASS
D-2	3'-6"x10'-0"	0'-0"	SOLID WOOD
D-2'	3'-6"x8'-0"	0'-0"	SOLID WOOD
D-3	3'-0"x10'-0"	0'-0"	SOLID WOOD
D-3'	3'-0"x8'-0"	0'-0"	SOLID WOOD
D-4	2'-6"x10'-0"	0'-0"	SOLID WOOD
D-4'	2'-6"x8'-0"	0'-0"	SOLID WOOD
W1	20'-0"x10'-6"	0'-6"	ALUMINUM+GLASS
W2	15'-6"x2'-0"	3'-0"	ALUMINUM+GLASS
W3	15'-0"x9'-6"	0'-6"	ALUMINUM+GLASS
W4	13'-6"x9'-6"	0'-6"	ALUMINUM+GLASS
W5	12'-0"x9'-6"	0'-6"	ALUMINUM+GLASS
W6	11'-0"x9'-6"	0'-6"	ALUMINUM+GLASS
W7	10'-0"x9'-6"	0'-6"	ALUMINUM+GLASS
W8	8'-10"x9'-6"	0'-6"	ALUMINUM+GLASS
W9	8'-0"x9'-6"	0'-6"	ALUMINUM+GLASS
W10	7'-10"x9'-6"	0'-6"	ALUMINUM+GLASS
W11	6'-0"x9'-6"	0'-6"	ALUMINUM+GLASS
W11'	6'-0"x3'-0"	5'-0"	ALUMINUM+GLASS
W12	5'-9"x9'-6"	0'-6"	ALUMINUM+GLASS
W12'	5'-9"x2'-0"	3'-0"	ALUMINUM+GLASS
W13	5'-6"x6'-0"	4'-0"	BLIND+GLASS
W13'	5'-6"x9'-6"	0'-6"	ALUMINUM+GLASS
W14	5'-0"x9'-6"	0'-6"	ALUMINUM+GLASS
W15	4'-0"x9'-6"	0'-6"	ALUMINUM+GLASS
W16	4'-0"x6'-0"	4'-0"	BLIND+GLASS
W17	3'-0"x9'-6"	0'-6"	ALUMINUM+GLASS
W18	3'-0"x6'-0"	4'-0"	ALUMINUM+GLASS
W18'	3'-0"x6'-0"	2'-0"	BLIND+GLASS
W19	1'-6"x6'-0"	4'-0"	BLIND+GLASS
W20	12'-6"x2'-0"	0'-6"	ALUMINUM+GLASS

TITLE.

PROPOSED BUILDING PLAN OF PLOT
NO. 588, STREET # 8-A SECTOR. M1,
LAKE CITY HOUSING SCHEME 13 KM.
RAIWIND RAOD LAHORE.

OWNER NAME :

MR. SAQIB AZIZ CHOUDHRY

OWNER SIGNATURE :

ARCHITECT SIGNATURE & STAMP :

PEC# CIVIL -

CONSULTANT NUMBER