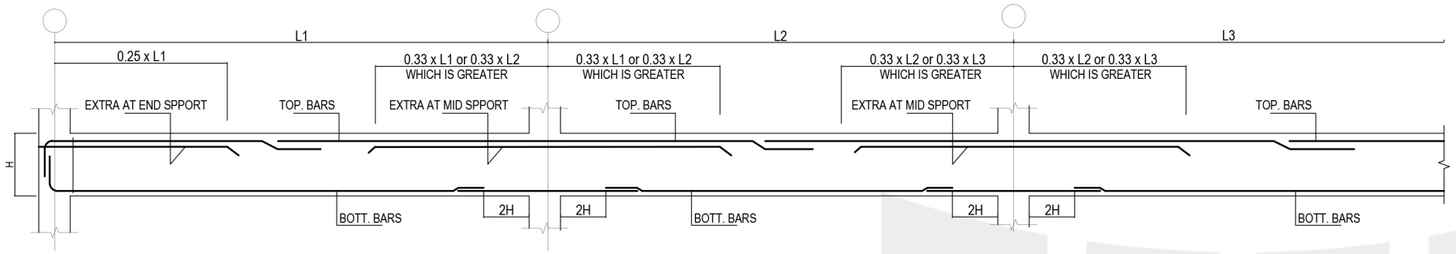

TYP BARS CUTOFF DETAILS FOR BEAM

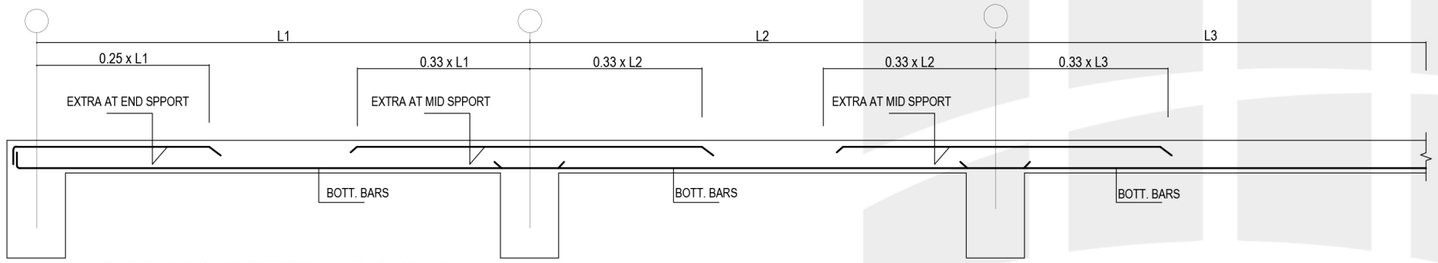

TYP BARS CUTOFF DETAILS FOR SLAB

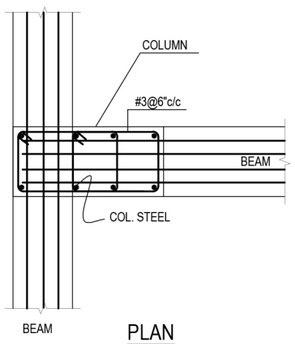

PLAN

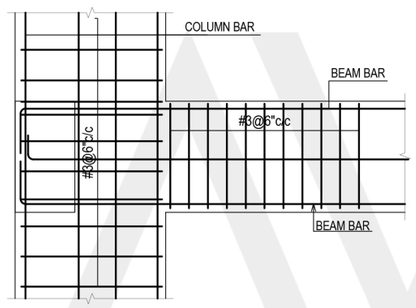

ELEVATION
TYP. JOINT DETAIL

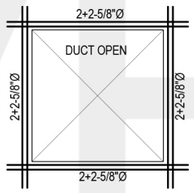

TYP. DUCT OPENING DETAIL

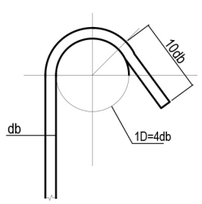

135° HOOK
(STIRRUPS & TIE REINF.)

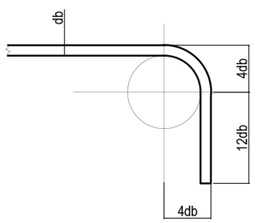

90° HOOK
(PRIMARY REINF.)

GENERAL NOTE:

1 - Reinforced cement concrete unless specified shall be design having 1:2:4 mix with cylinder strength 3000 Psi at 28 days for all concrete elements

2 - Reinforced bars to be used are shall be of deformed steel with minimum yield strength of 60000 psi.

3 - Lap in reinforcing bars must be staggered minimum lap in tension shall be 60 x diameter of bar.

4- Maximum size of the coarse aggregate shall be 3/4"or 19mm in foundations and 1/2"or 12mm at other wise.

5 - All excavation pits shall be inspected by the engineer / authorized representative before pouring concrete.

6 - Depth of foundations are as shown in drawings.

7 - Clear cover to reinforcement to be:

a) Foundation = 2"

b) Beam = 1-1/2"

c) Slab & Staircase = 3/4"

SCHEDULE OF LINTELS

CLEAR SPAN	CONFIGURATION	
UPTO 4'-0"	9" × 9", 2-#4, #3@4"-8"c/c, 2-#4	41/2" × 9", 2-#4, #3@4"-8"c/c, 2-#4
UPTO 6'-0"	9" × 12", 2-#4, #3@4"-8"c/c, 3-#4	41/2" × 9", 2-#4, #3@4"-8"c/c, 2-#4
UPTO 8'-0"	9" × 12", 2-#4, #3@4"-8"c/c, 3-#4	41/2" × 12", 2-#4, #3@4"-8"c/c, 2-#4
UPTO 10'-0"	9" × 15", 2-#4, #3@4"-8"c/c, 4-#4	41/2" × 15", 2-#4, #3@4"-8"c/c, 5-#4
TYP. Lintel Detail On All Walls	9" × 9", 2-#4, #3@4"-8"c/c, 2-#4	41/2" × 9", 2-#4, #3@4"-8"c/c, 2-#4

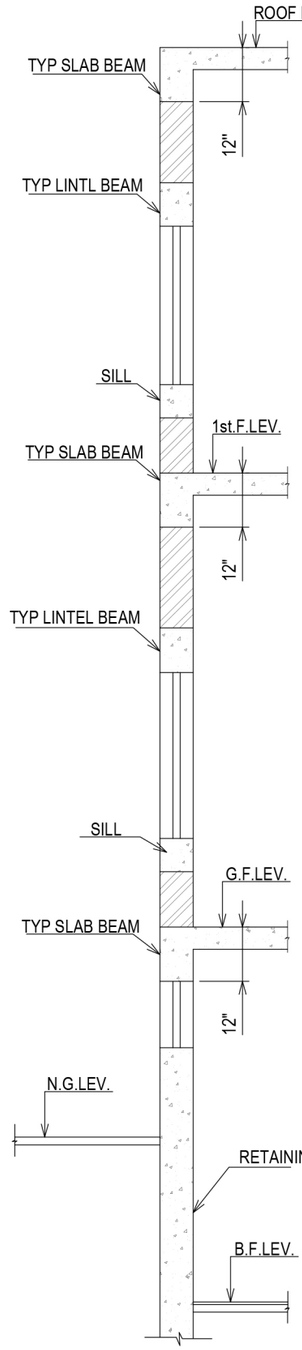

TYP. SECTION OF WALL

TYPICAL LINTEL SLAB LEV. BEAM DETAILS UNLESS SPECIFED ON ALL WALL

TITLE: GENERAL STRUCTURE NOTES	PROJECT: PLOT # 588, STREET 8-A, SECTOR M1, LAKE CITY, LAHORE.	DESIGN CONSULTANT:	STRUCTURE CONSULTANT:

DESIGNED BY:		DRAWN BY:		DWG: G-01
DATE:	26-01-2026			
REVISION DATE:	00-00-0000	00		
SCALE:	AS SHOWN			

AVENUE DEVELOPMENTS

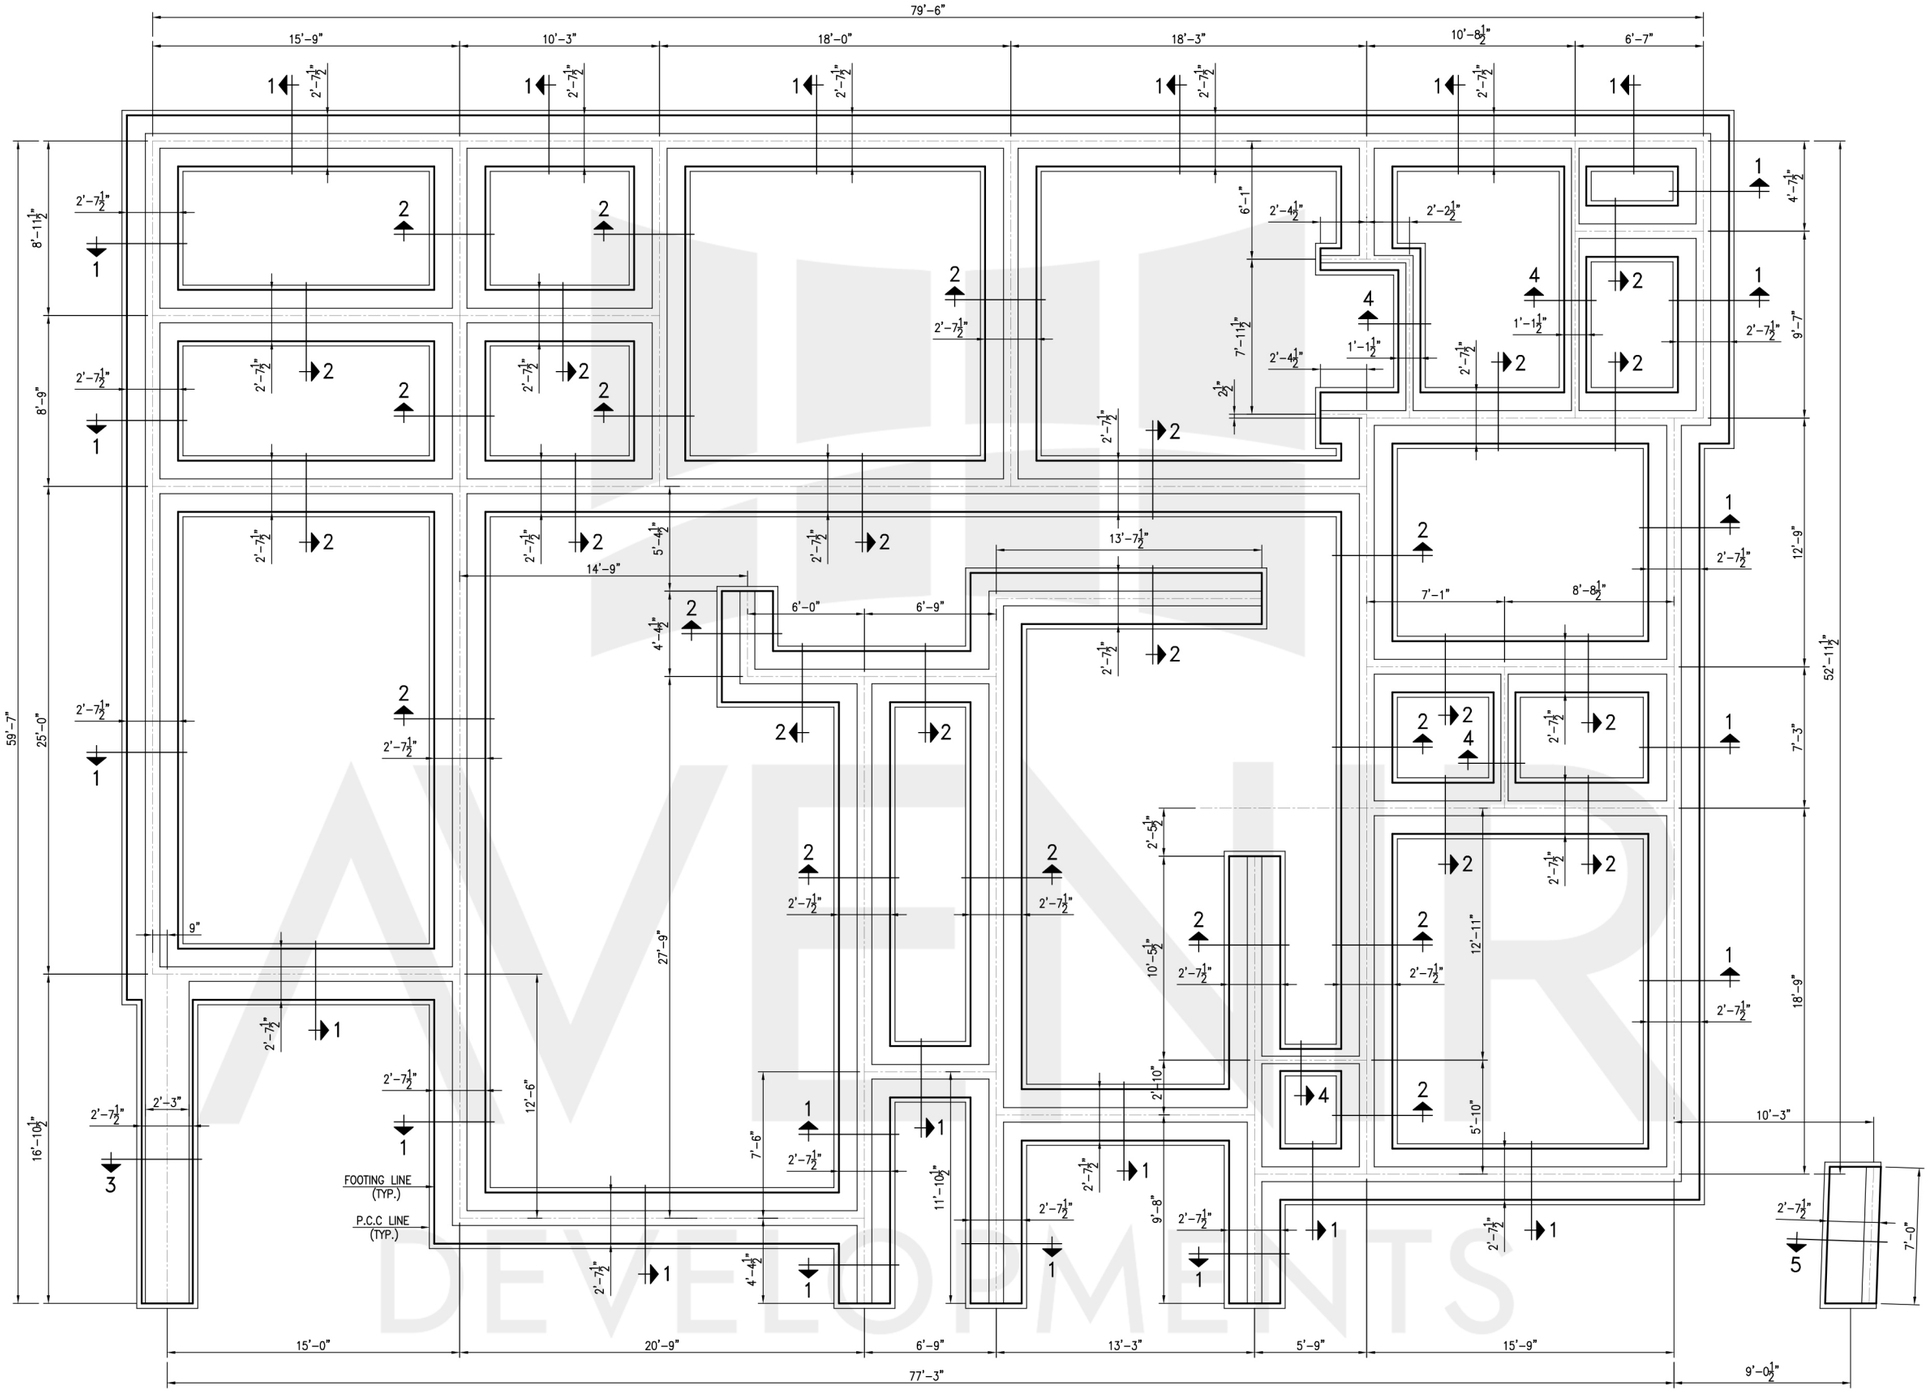

FOOTING LAYOUT PLAN

TITLE: FOOTING LAYOUT PLAN	PROJECT: PLOT # 588, STREET 8-A, SECTOR M1, LAKE CITY, LAHORE.	DESIGN CONSULTANT:	STRUCTURE CONSULTANT:	DESIGNED BY:	DRAWN BY:	DWG: S-01
				DATE:	26-01-2026	
				REVISION DATE:	00-00-0000 / 00	
				SCALE:	AS SHOWN	

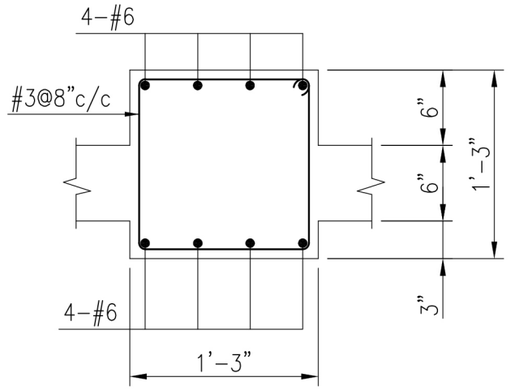

BEAM RB–21

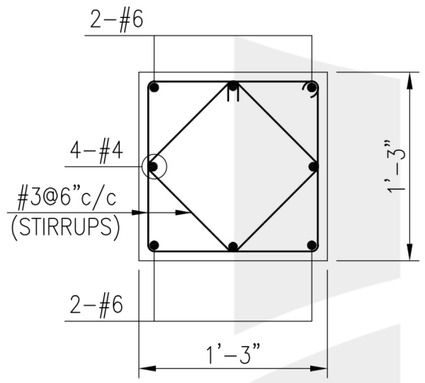

SECTION X–X

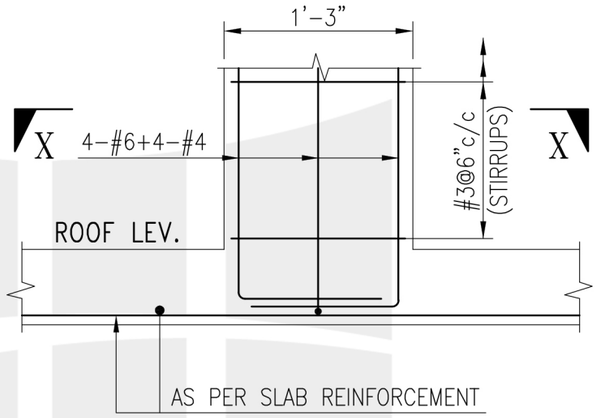

TYP. COLUMN C–X SECTIONAL DETAIL FOR O.H. WATER TANK

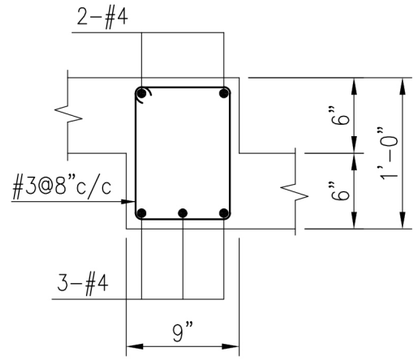

CONCEALED BEAM CB–1

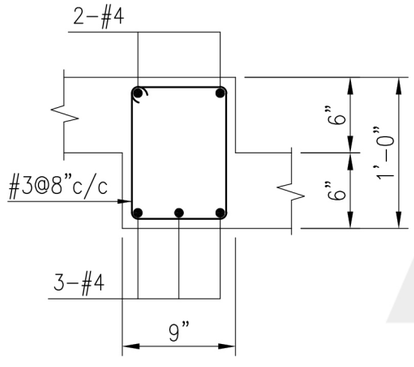

CONCEALED BEAM CB–2
(SECTION 2–2)

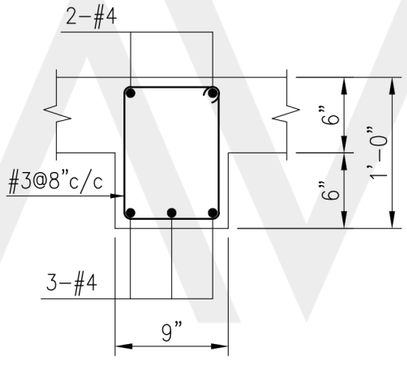

CONCEALED BEAM CB–2
(SECTION 2A–2A)

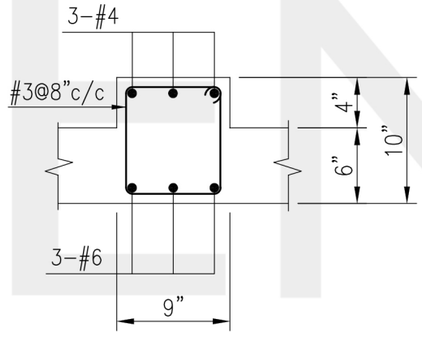

CONCEALED BEAM CB–3

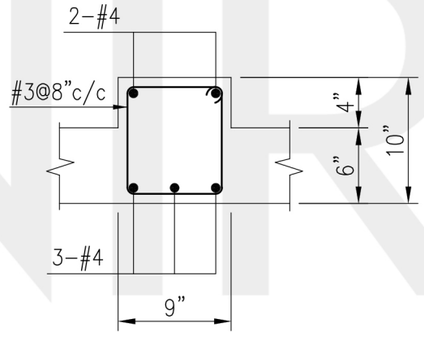

CONCEALED BEAM CB–4

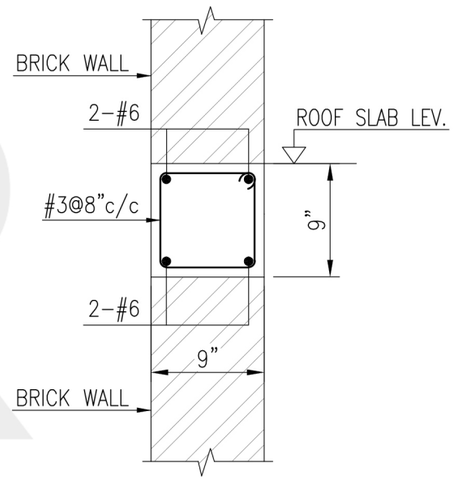

TYP. TIE BEAM

AVENUE DEVELOPMENTS

TITLE: BEAMS REINFORCEMENT DETAIL (ROOF SLAB) (BEAMS RB-21 & CB-1 TO CB-4)	PROJECT: PLOT # 588, STREET 8-A, SECTOR M1, LAKE CITY, LAHORE.	DESIGN CONSULTANT:	STRUCTURE CONSULTANT:	DESIGNED BY:		DRAWN BY:	DWG: S-10
				DATE:	26-01-2026		
				REVISION DATE:	00-00-0000	00	
				SCALE:	AS SHOWN		

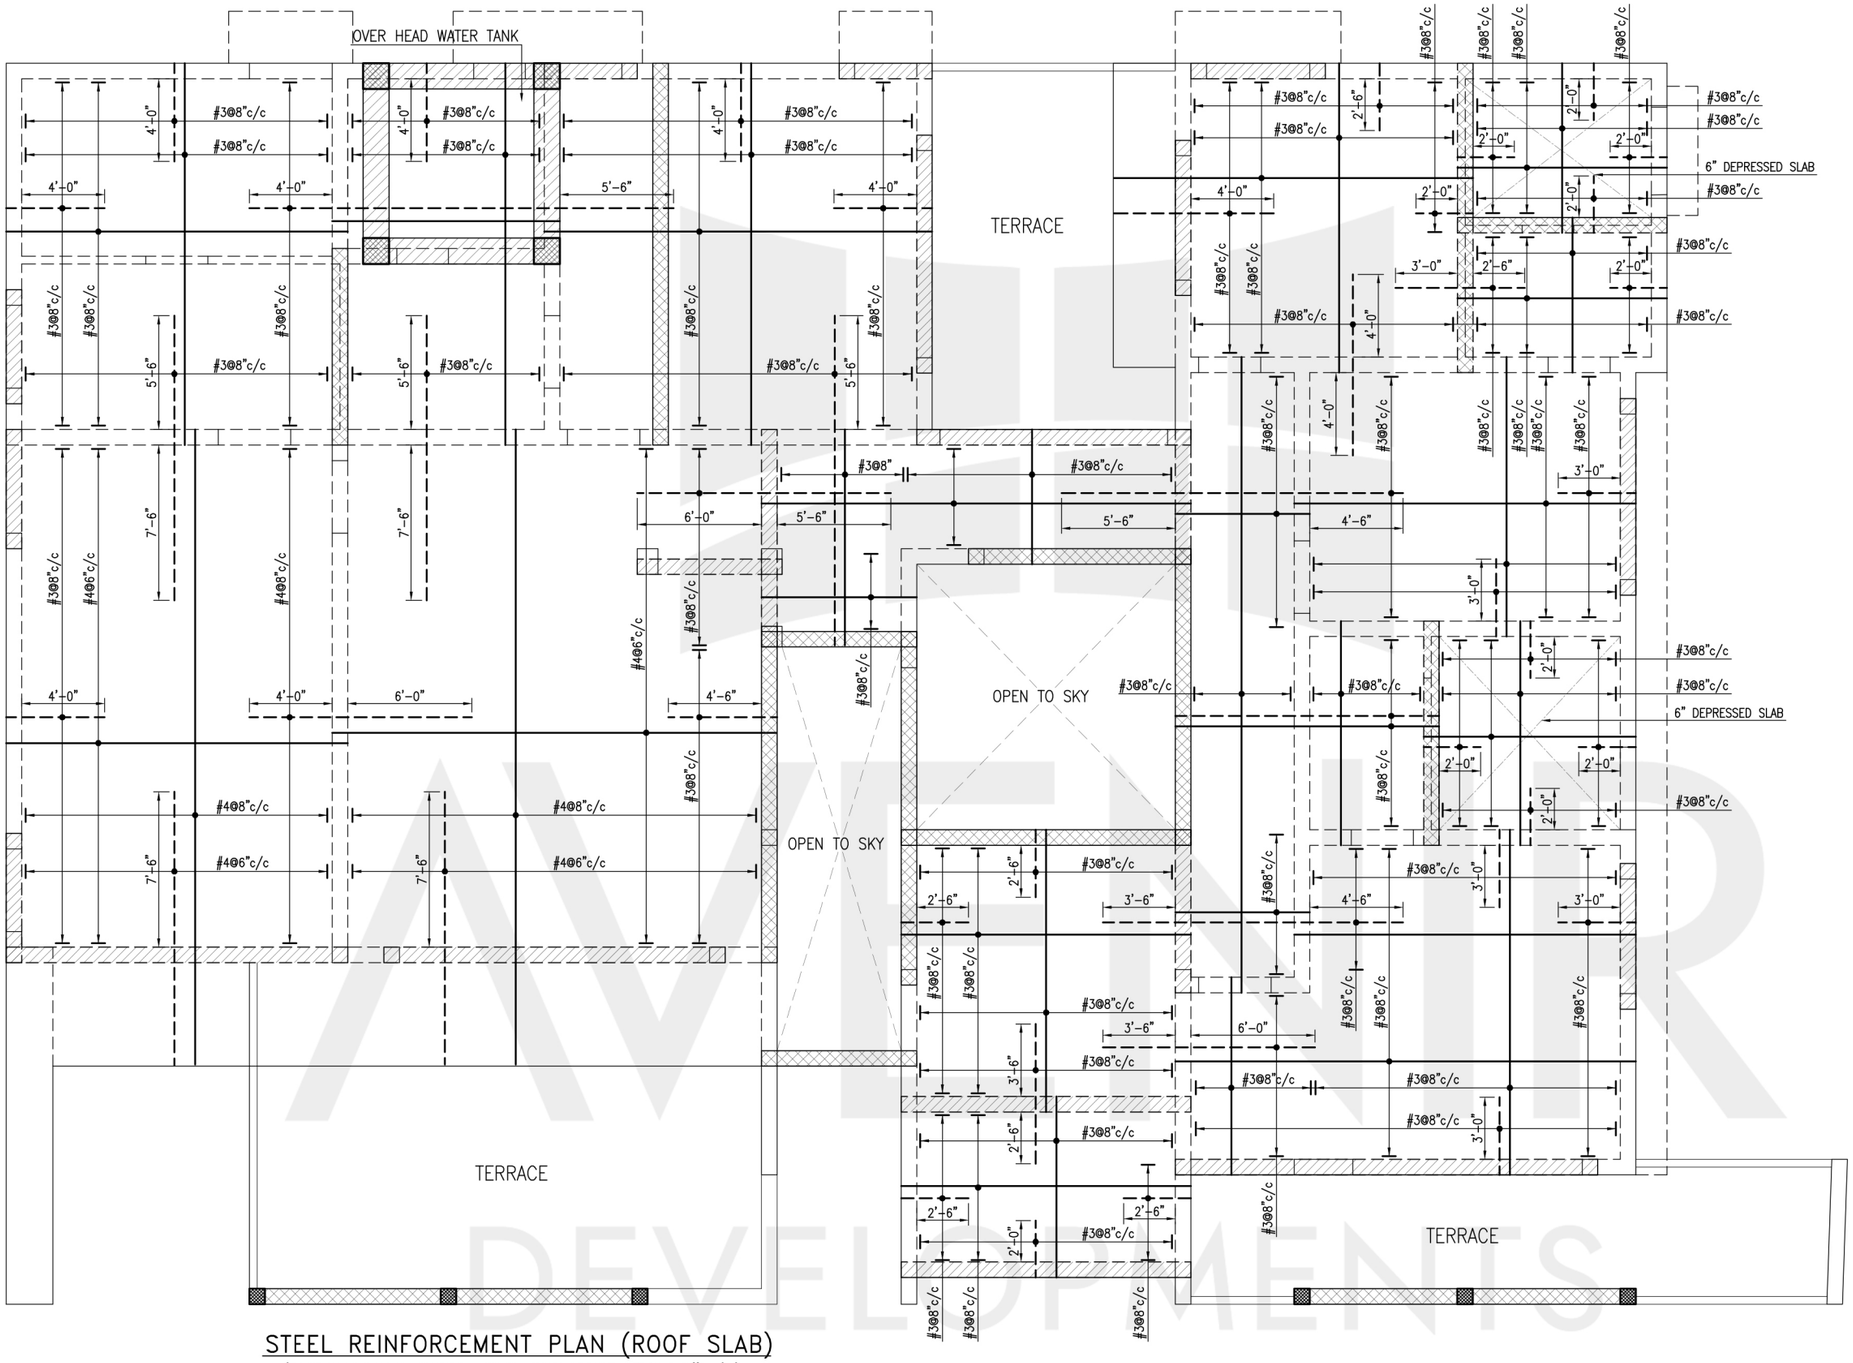

LEGEND:–

——— INDICATES BOTTOM BAR

– – – – INDICATES TOP BAR

T&B INDICATES TOP & BOTTOM

STEEL REINFORCEMENT PLAN (ROOF SLAB)

(DISTRIBUTION STEEL FOR TOP BARS #3@12"c/c)

(SLAB THICKNESS =6" UNLESS NOTED OTHERWISE)

TITLE: STEEL REINFORCEMENT PLAN (ROOF SLAB)	PROJECT: PLOT # 588, STREET 8-A, SECTOR M1, LAKE CITY, LAHORE.	DESIGN CONSULTANT:	STRUCTURE CONSULTANT:	DESIGNED BY:		DRAWN BY:	DWG: S-11
				DATE:	26-01-2026		
				REVISION DATE:	00-00-0000	00	
				SCALE:	AS SHOWN		

AVENIR DEVELOPMENTS

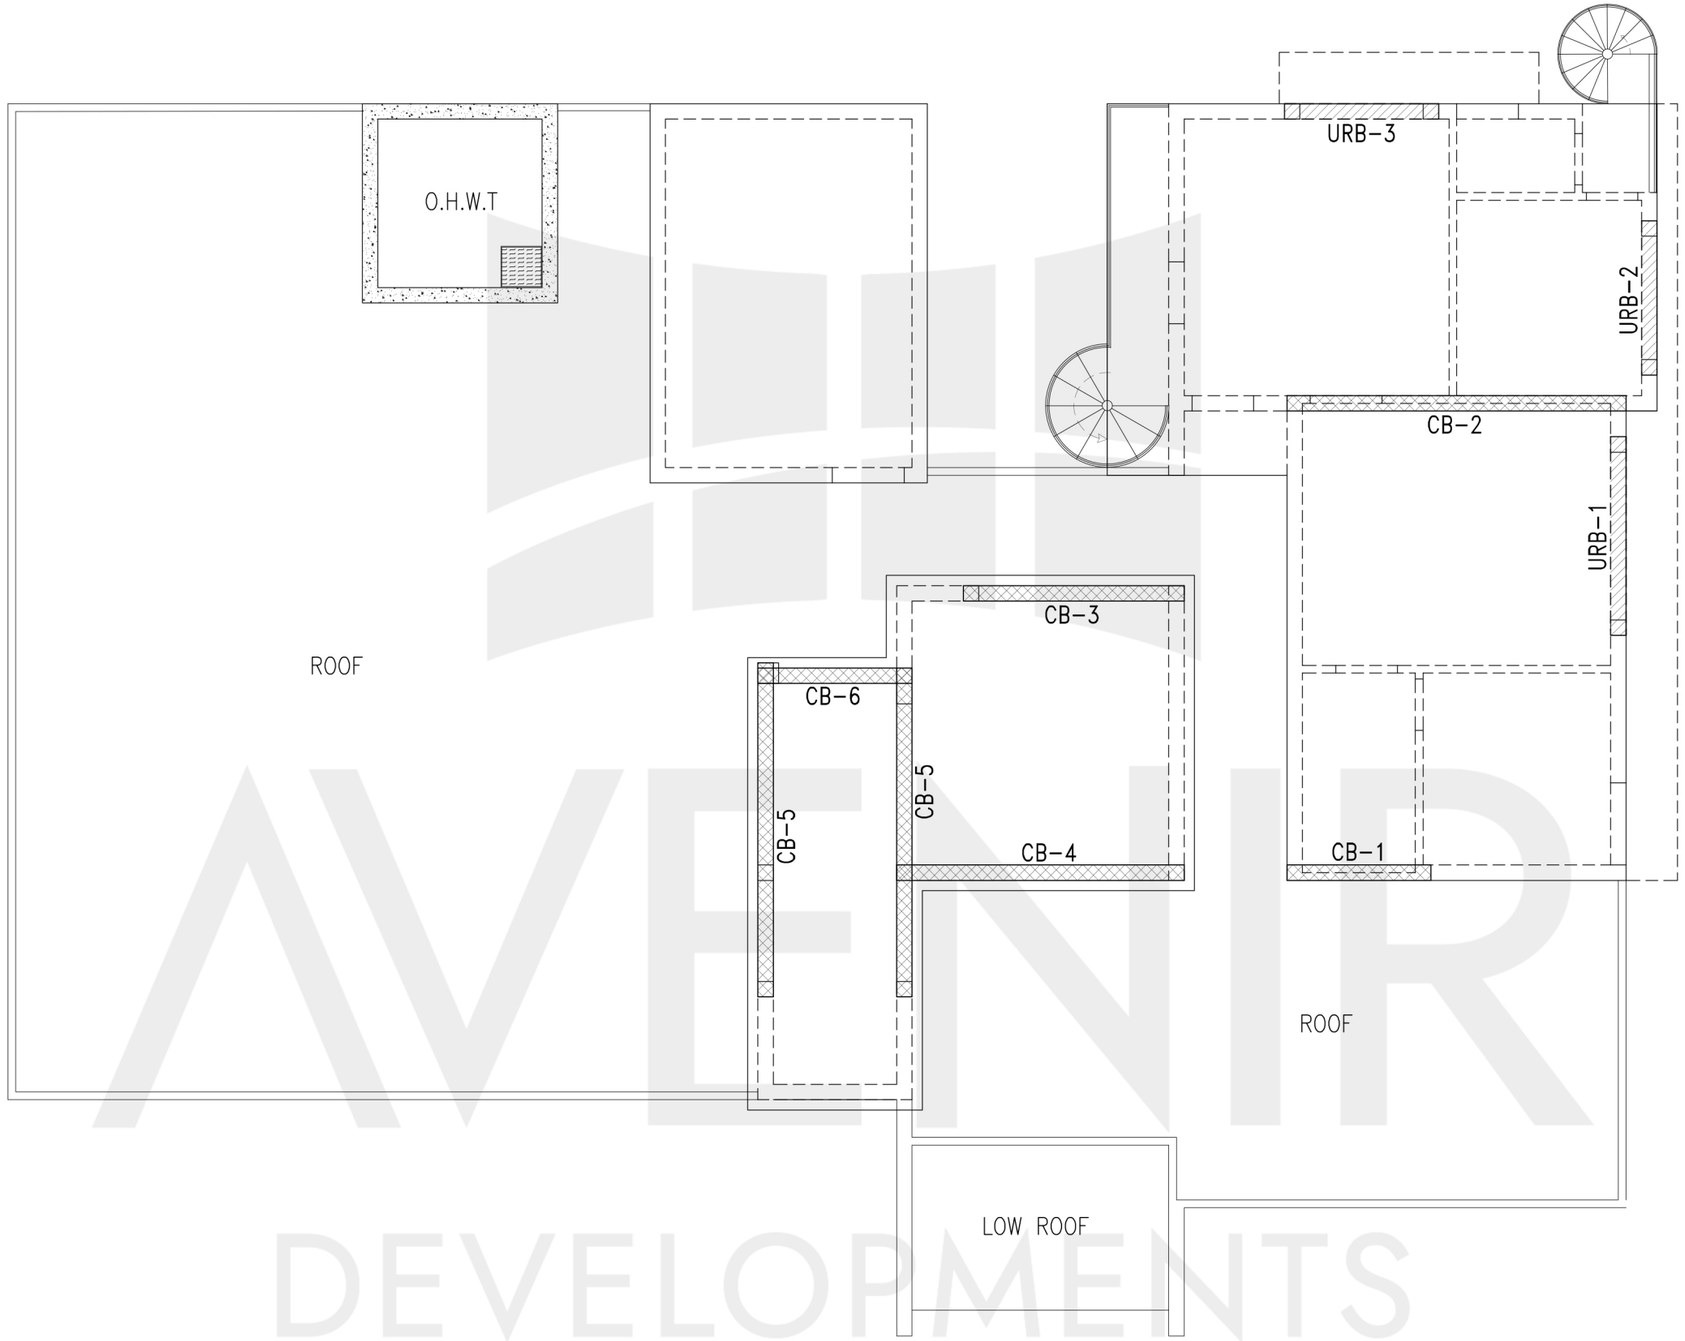

BEAMS FRAMING PLAN (UPPER ROOF SLAB)

TITLE: BEAMS FRAMING PLAN (UPPER ROOF SLAB)	PROJECT: PLOT # 588, STREET 8-A, SECTOR M1, LAKE CITY, LAHORE.	DESIGN CONSULTANT:	STRUCTURE CONSULTANT:	DESIGNED BY:		DRAWN BY:	DWG: S-12
				DATE:	26-01-2026		
				REVISION DATE:	00-00-0000	00	
				SCALE:	AS SHOWN		

AVENIR DEVELOPMENTS

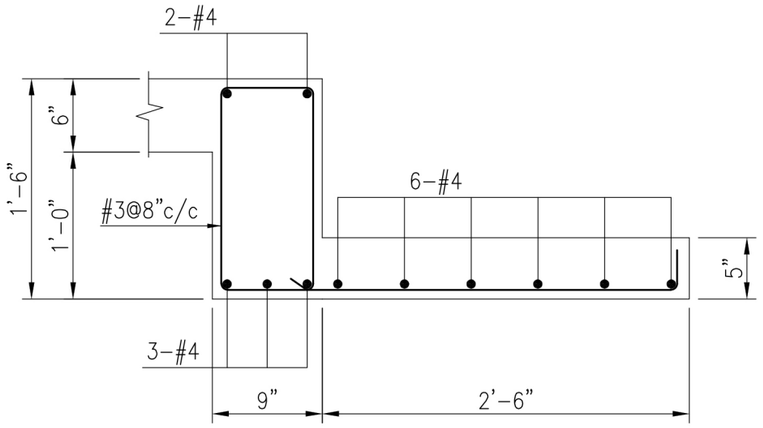

BEAM URB-1

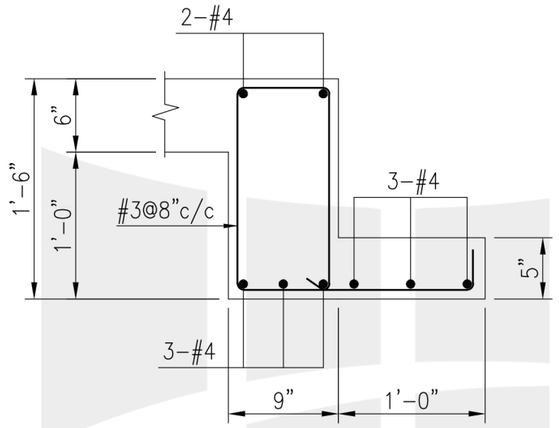

BEAM URB-2

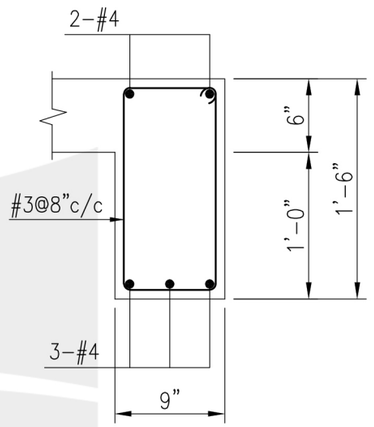

BEAM URB-3

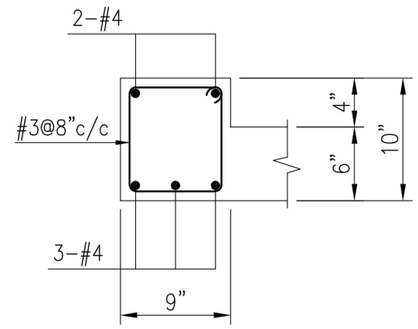

CONCEALED BEAM CB-1

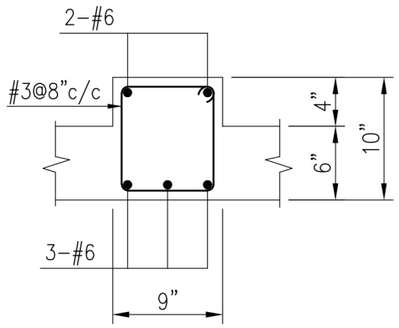

CONCEALED BEAM CB-2

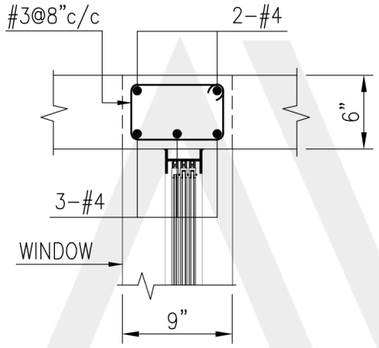

CONCEALED BEAM CB-3

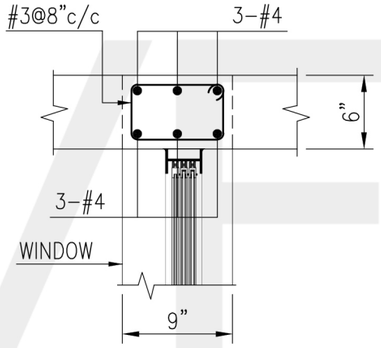

CONCEALED BEAM CB-4

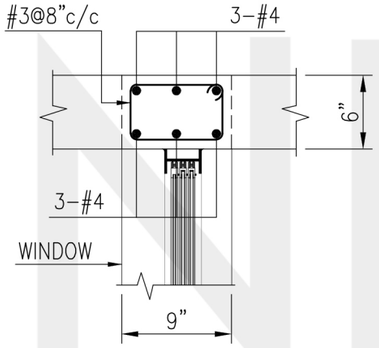

CONCEALED BEAM CB-5

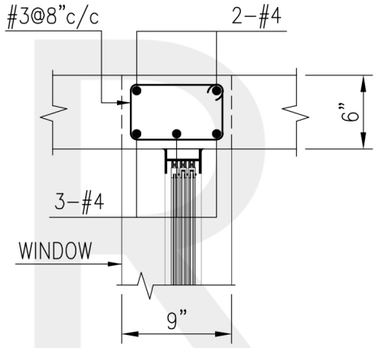

CONCEALED BEAM CB-6

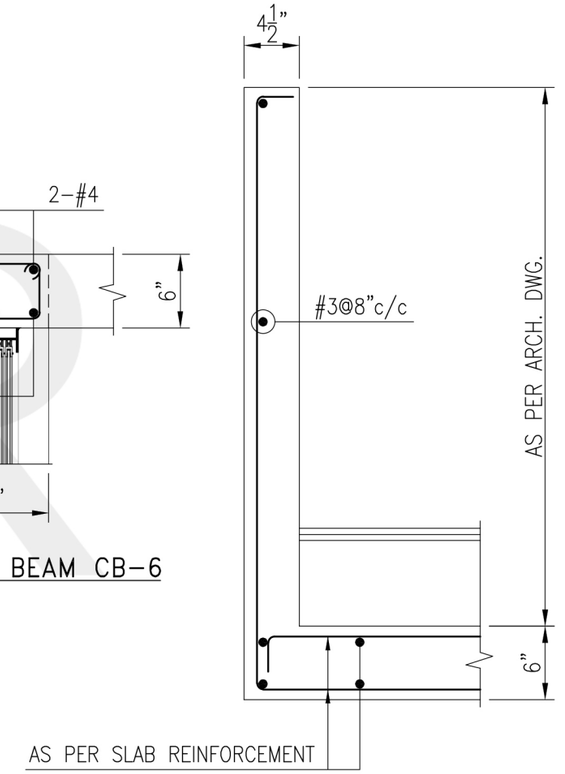

TYP. PARAPET WALL SECTION

TITLE: BEAMS REINFORCEMENT DETAIL (UPPER ROOF SLAB) (BEAMS URB-1 TO URB-3 & CB-1 TO CB-6)	PROJECT: PLOT # 588, STREET 8-A, SECTOR M1, LAKE CITY, LAHORE.	DESIGN CONSULTANT:	STRUCTURE CONSULTANT:	DESIGNED BY:		DRAWN BY:	DWG: S-13
				DATE:	26-01-2026		
				REVISION DATE:	00-00-0000	00	
				SCALE:	AS SHOWN		

AVENIR DEVELOPMENTS

LEGEND:–

——— INDICATES BOTTOM BAR

– – – – INDICATES TOP BAR

T&B INDICATES TOP & BOTTOM

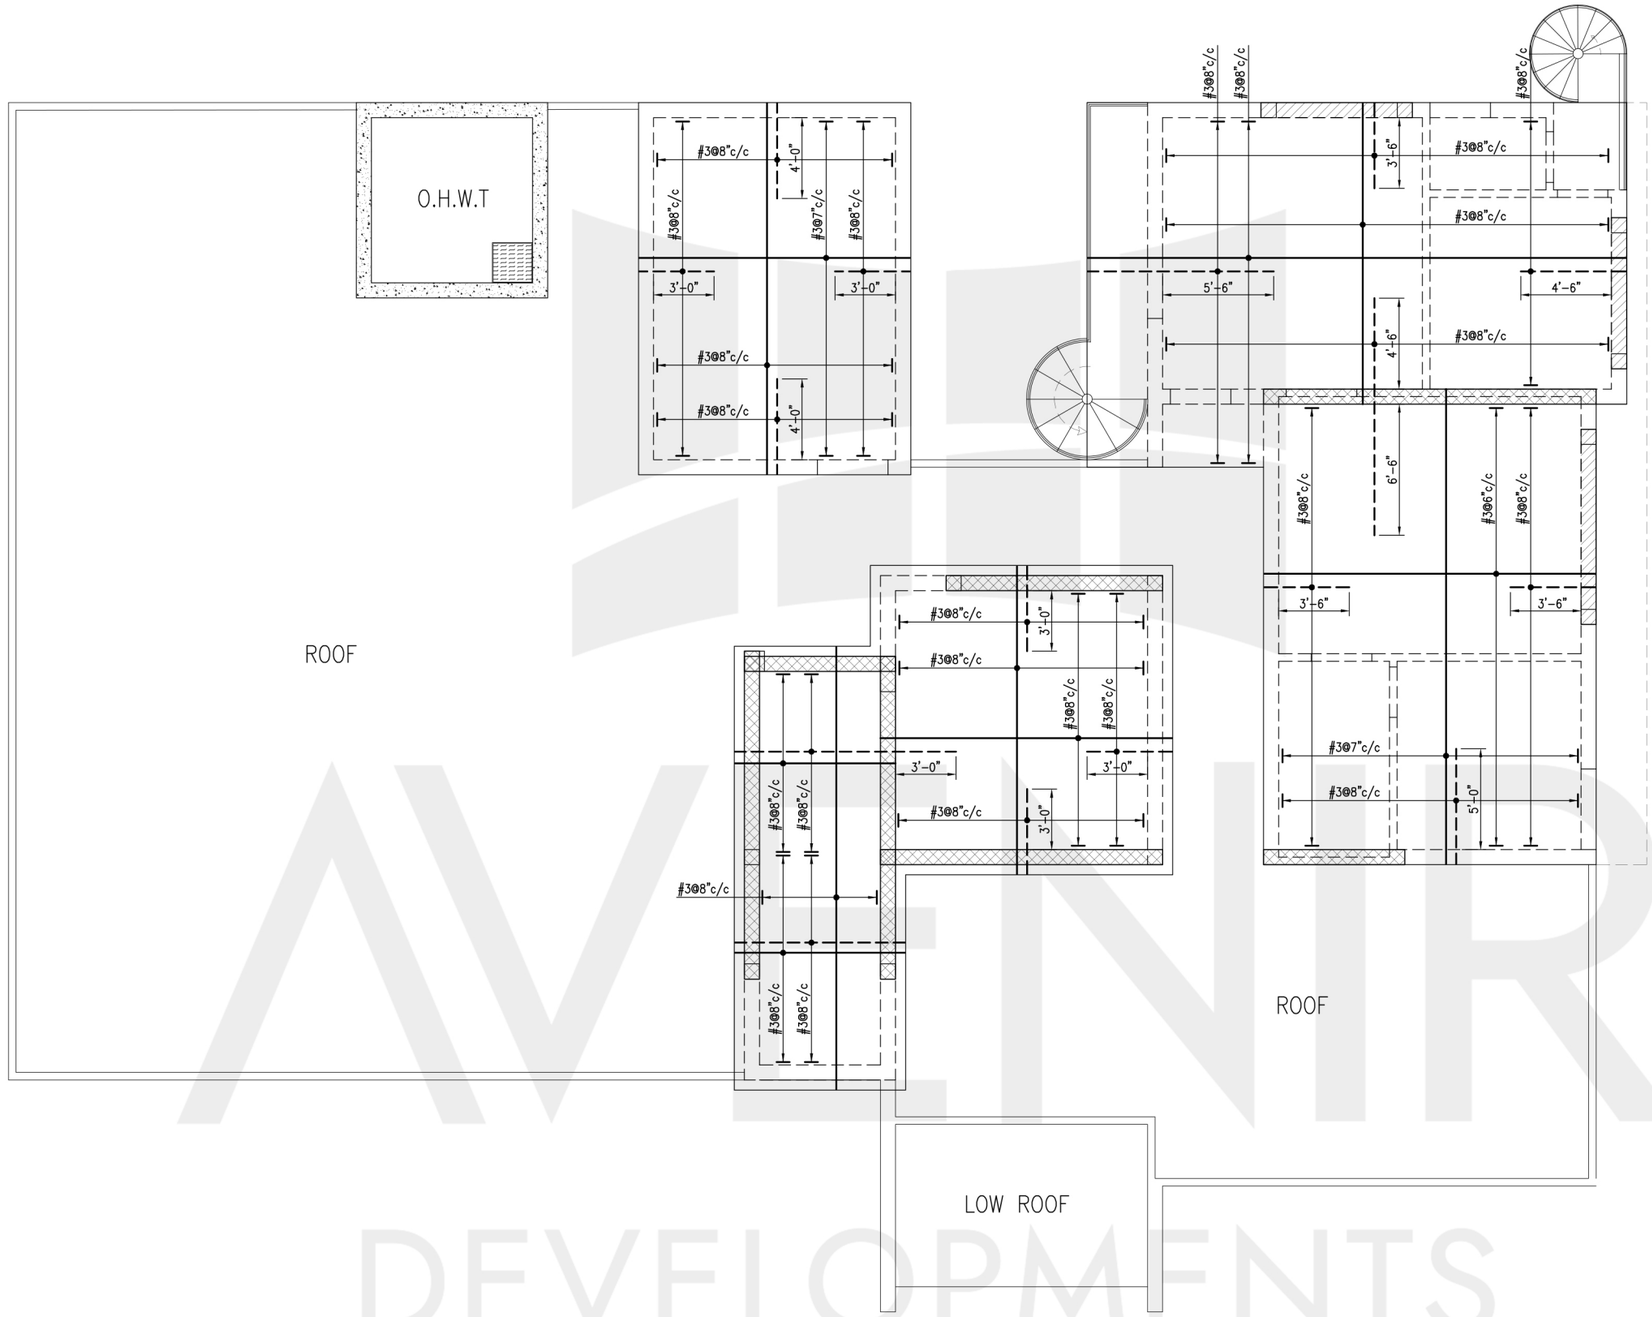

STEEL REINFORCEMENT PLAN (UPPER ROOF SLAB)

(DISTRIBUTION STEEL FOR TOP BARS #3@12"c/c)

(SLAB THICKNESS =6" UNLESS NOTED OTHERWISE)

TITLE: STEEL REINFORCEMENT PLAN (UPPER ROOF SLAB)	PROJECT: PLOT # 588, STREET 8-A, SECTOR M1, LAKE CITY, LAHORE.	DESIGN CONSULTANT:	STRUCTURE CONSULTANT:	DESIGNED BY:		DRAWN BY:	DWG: S-14
				DATE:	26-01-2026		
				REVISION DATE:	00-00-0000	00	
				SCALE:	AS SHOWN		

AVENIR DEVELOPMENTS

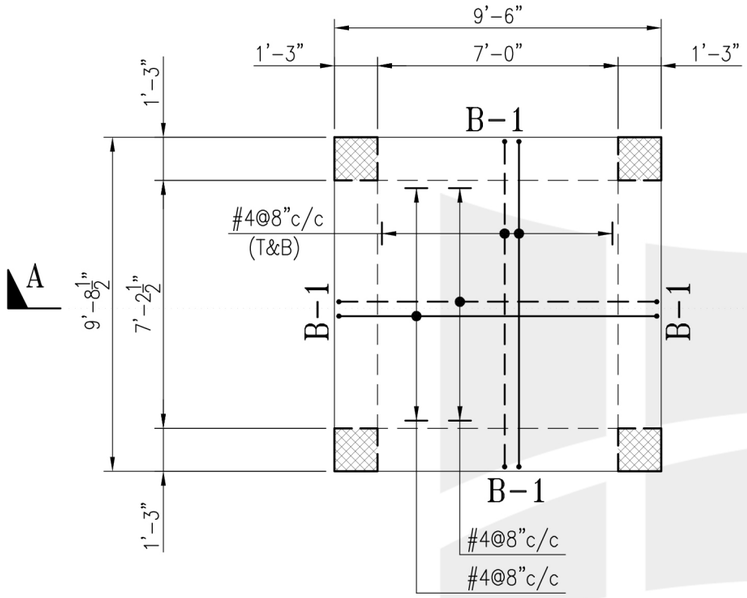

BOTTOM SLAB REINFORCEMENT PLAN
FOR O.H. WATER TANK
(SLAB THICKNESS=8")

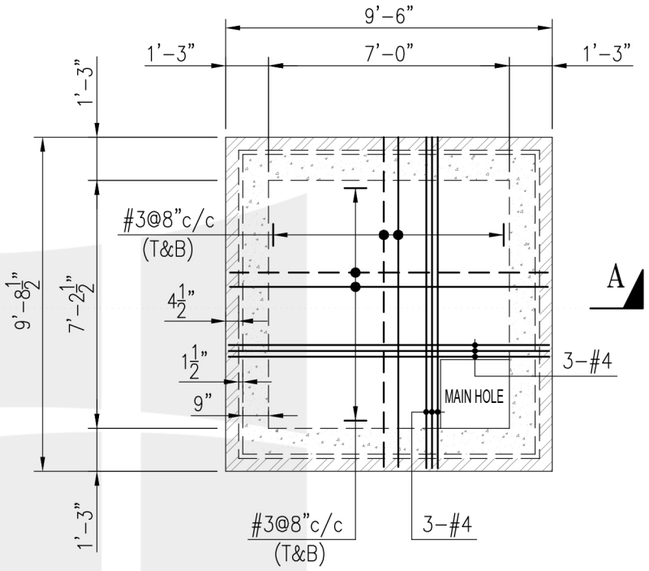

TOP SLAB REINFORCEMENT PLAN
FOR O.H. WATER TANK
(SLAB THICKNESS=6")

LEGEND:-

———	INDICATES BOTTOM BAR
- - - - -	INDICATES TOP BAR
T&B	INDICATES TOP & BOTTOM

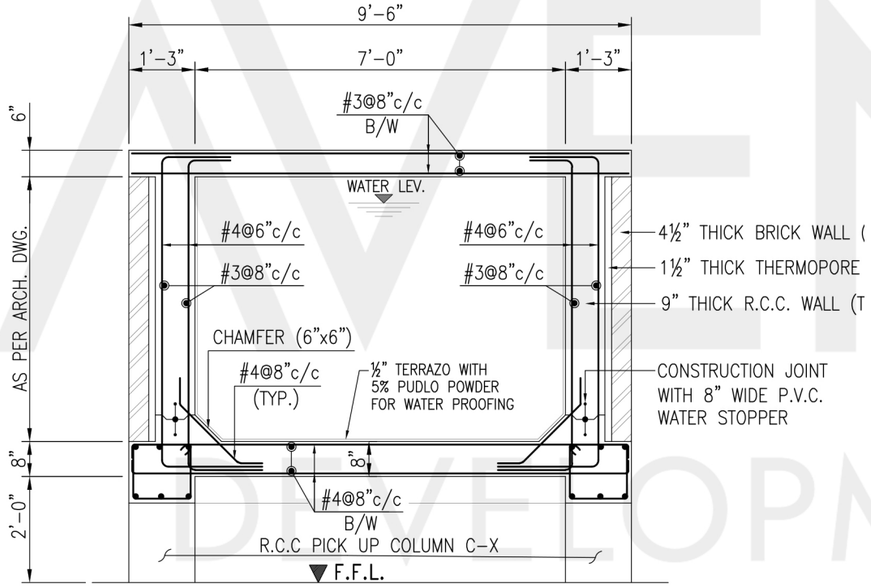

SECTION A-A

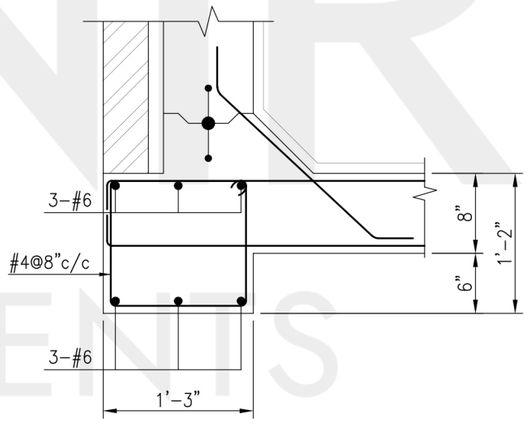

BEAM B-1

TITLE: STEEL REINFORCEMENT PLAN & SECTIONS FOR OVER HEAD WATER TANK	PROJECT: PLOT # 588, STREET 8-A, SECTOR M1, LAKE CITY, LAHORE.	DESIGN CONSULTANT:	STRUCTURE CONSULTANT:	DESIGNED BY:		DRAWN BY:	DWG: S-15
				DATE:	26-01-2026		
				REVISION DATE:	00-00-0000	00	
				SCALE:	AS SHOWN		

AVENUE DEVELOPMENTS

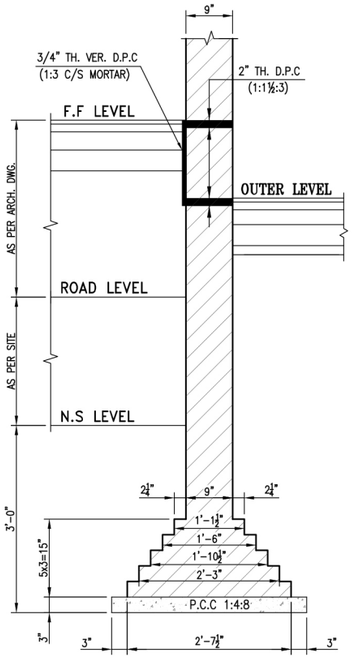

SECTION 1–1

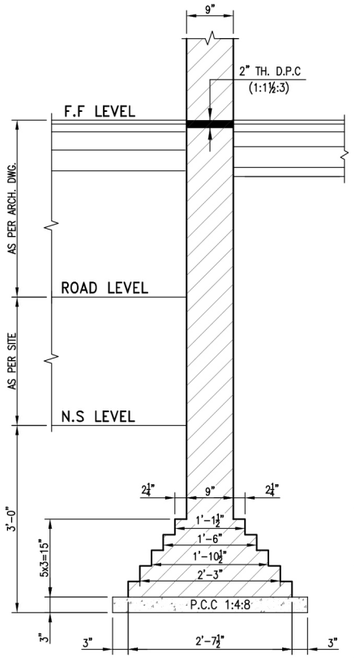

SECTION 2–2

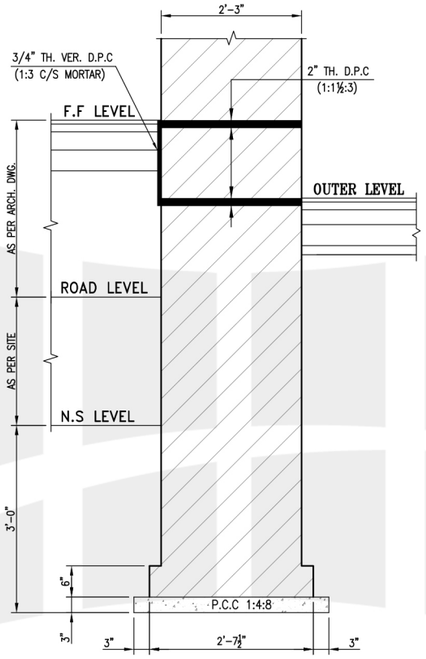

SECTION 3–3

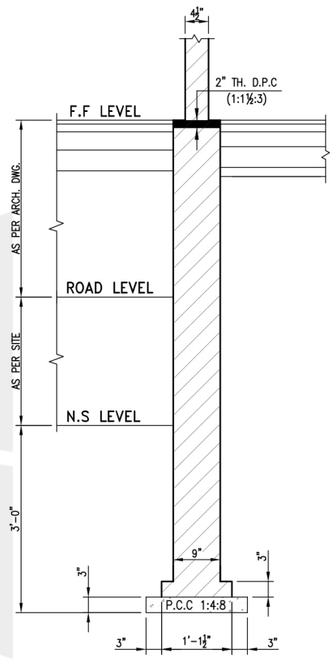

SECTION 4–4

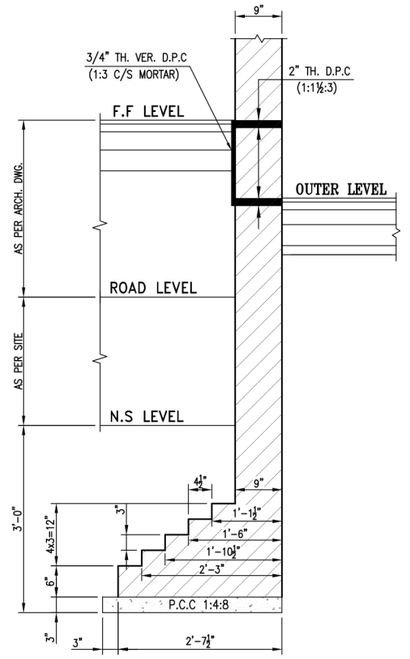

SECTION 5–5

TYP. BOUNDARY LOW HEIGHT WALL SECTION

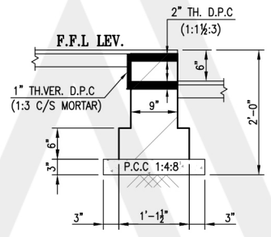

TYP. TOE WALL SECTION

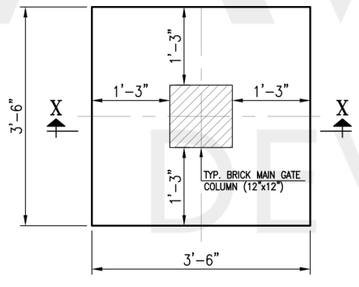

TYP. FOOTING PLAN FOR MAIN GATE COLUMN

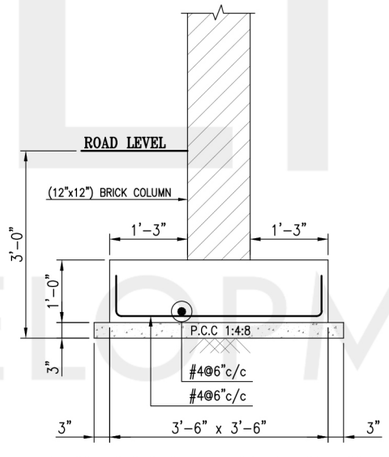

TYP. FOOTING SECTION X–X FOR MAIN GATE COLUMN

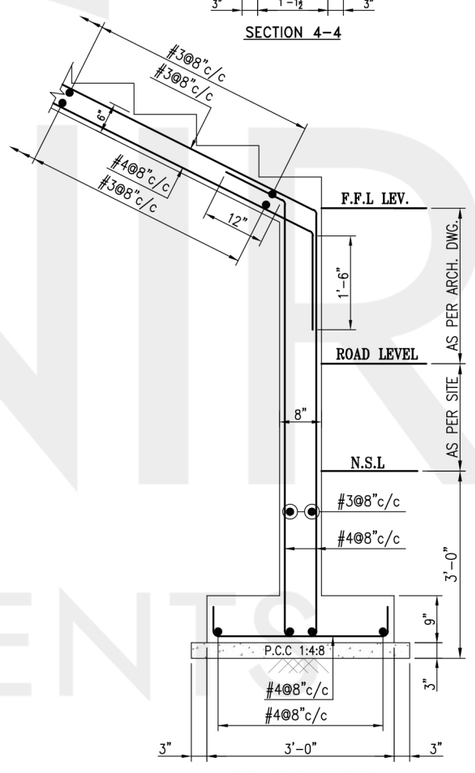

TYP. STAIR SECTION

TITLE: FOOTING SECTIONS	PROJECT: PLOT # 588, STREET 8-A, SECTOR M1, LAKE CITY, LAHORE.	DESIGN CONSULTANT:	STRUCTURE CONSULTANT:	DESIGNED BY:		DRAWN BY:	DWG: S-02
				DATE:	26-01-2026		
				REVISION DATE:	00-00-0000	00	
				SCALE:	AS SHOWN		

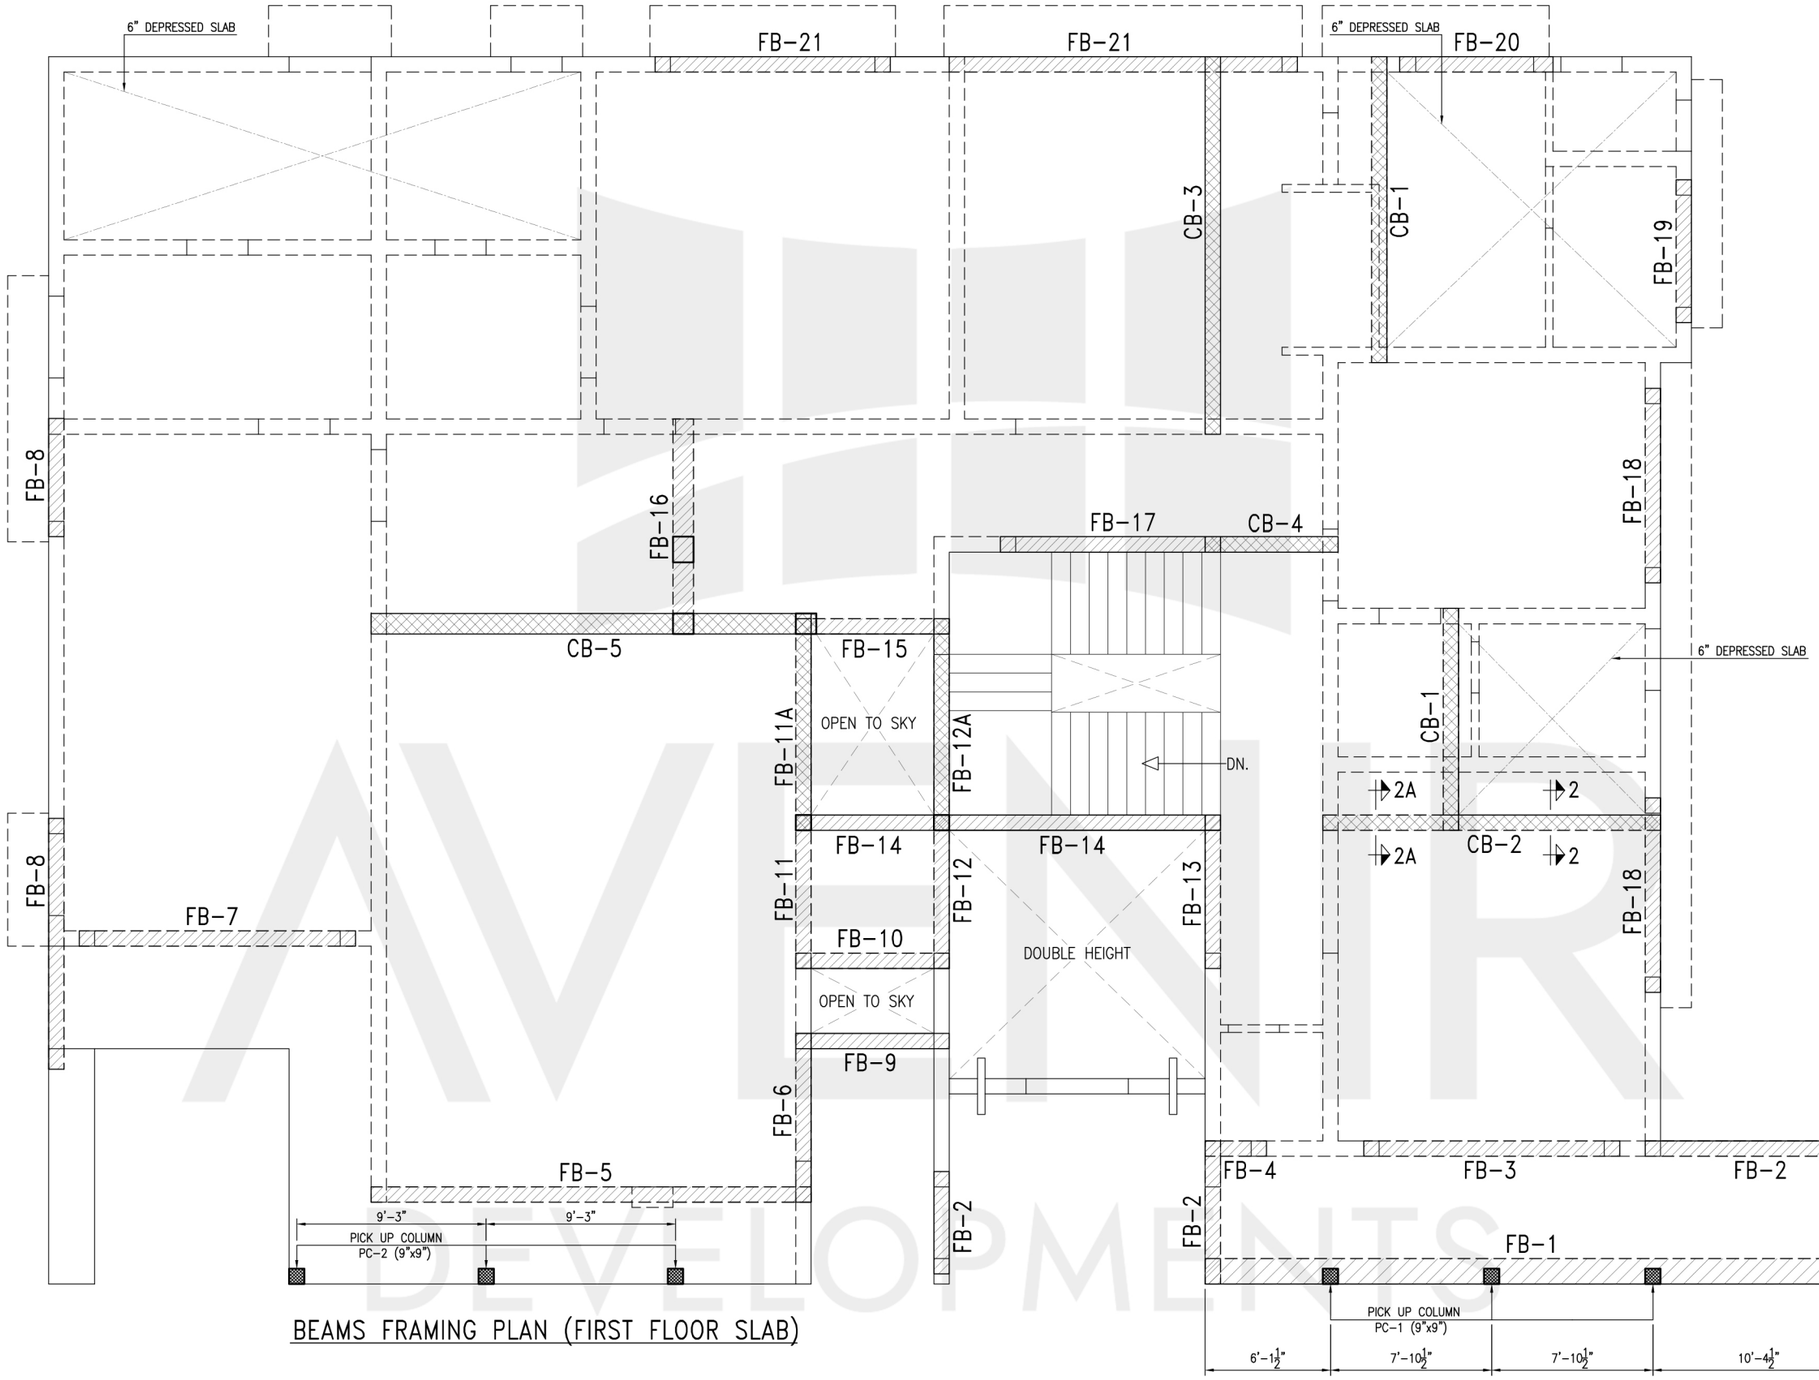

BEAMS FRAMING PLAN (FIRST FLOOR SLAB)

TITLE: BEAMS FRAMING PLAN (FIRST FLOOR SLAB)	PROJECT: PLOT # 588, STREET 8-A, SECTOR M1, LAKE CITY, LAHORE.	DESIGN CONSULTANT:	STRUCTURE CONSULTANT:	DESIGNED BY:	DRAWN BY:	DWG: S-03
				DATE:	26-01-2026	
				REVISION DATE:	00-00-0000 (00)	
				SCALE:	AS SHOWN	

AVENIR DEVELOPMENTS

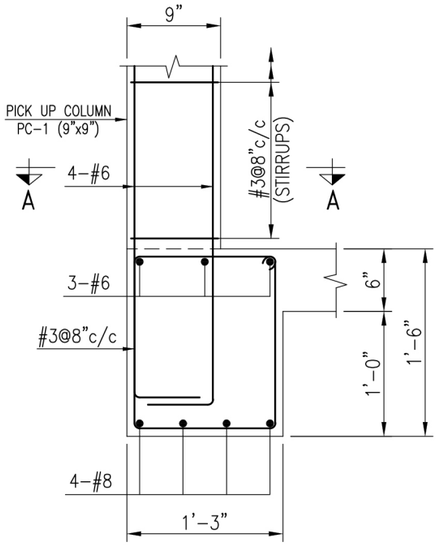

BEAM FB-1

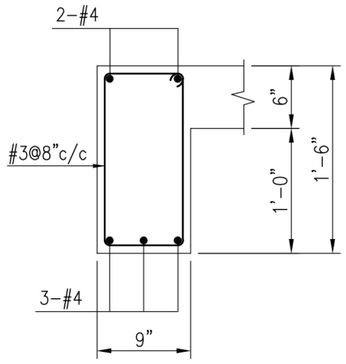

BEAM FB-2

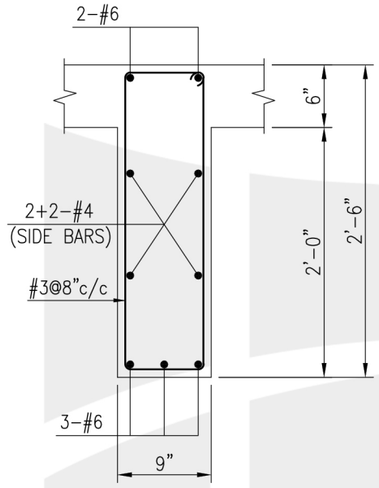

BEAM FB-3

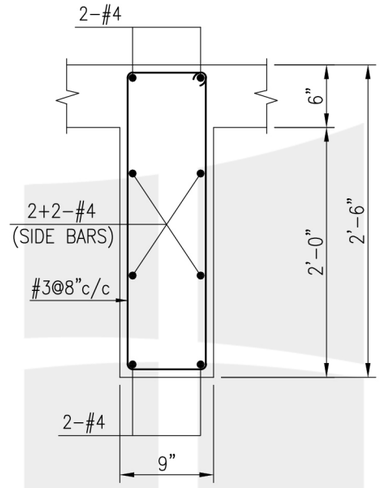

BEAM FB-4

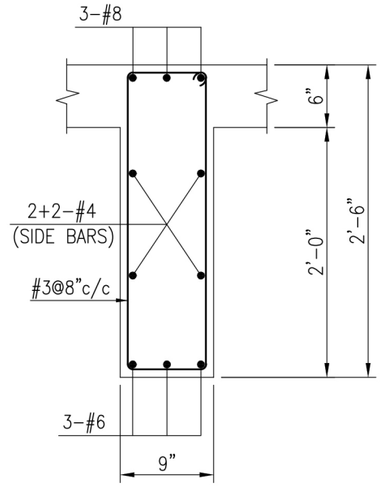

BEAM FB-5

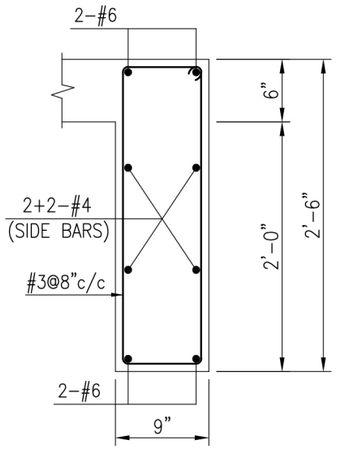

BEAM FB-6

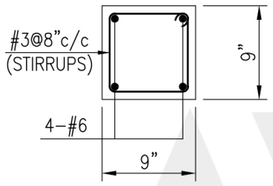

TYP. PICK UP COLUMN PC-1
(SECTION A-A)

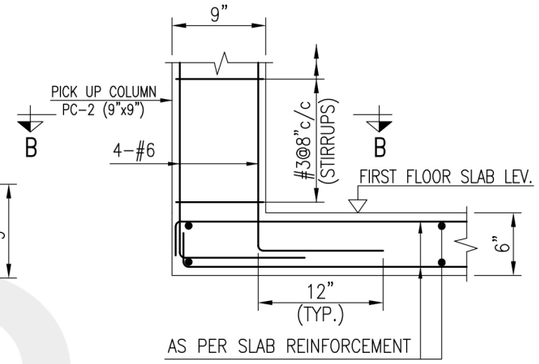

TYP. PICK UP COLUMN PC-2
SECTIONAL DETAIL

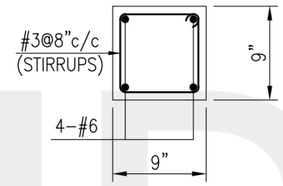

TYP. PICK UP COLUMN PC-2
(SECTION B-B)

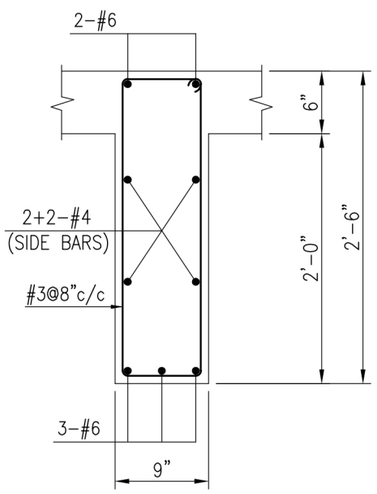

BEAM FB-7

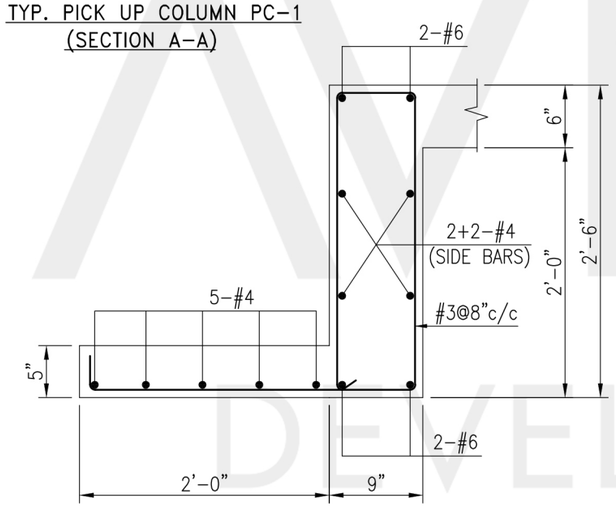

BEAM FB-8

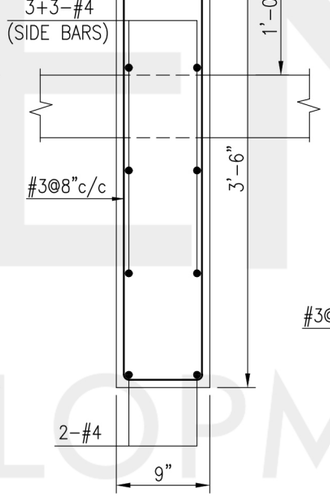

BEAM FB-9

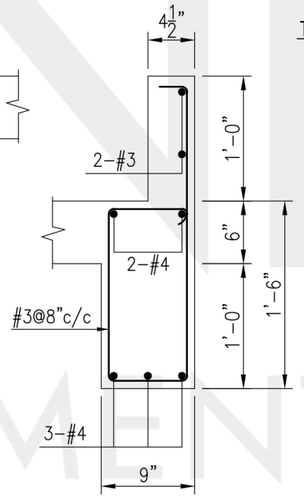

BEAM FB-10

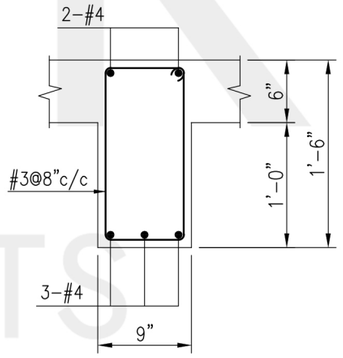

BEAM FB-11

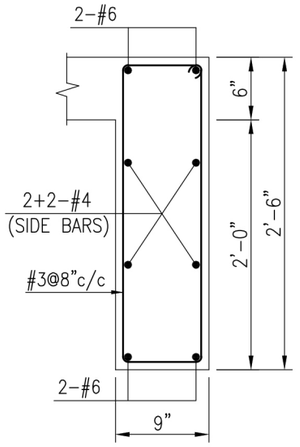

BEAM FB-11A

TITLE: BEAMS REINFORCEMENT DETAIL (FIRST FLOOR SLAB) (BEAMS FB-1 TO FB-11)	PROJECT: PLOT # 588, STREET 8-A, SECTOR M1, LAKE CITY, LAHORE.	DESIGN CONSULTANT:	STRUCTURE CONSULTANT:

DESIGNED BY:		DRAWN BY:	
DATE:	26-01-2026		
REVISION DATE:	00-00-0000	00	
SCALE:	AS SHOWN		

DWG: S-04

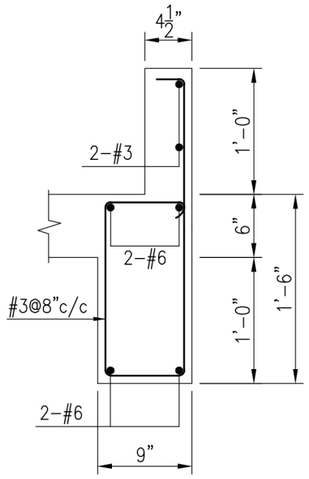

BEAM FB-12

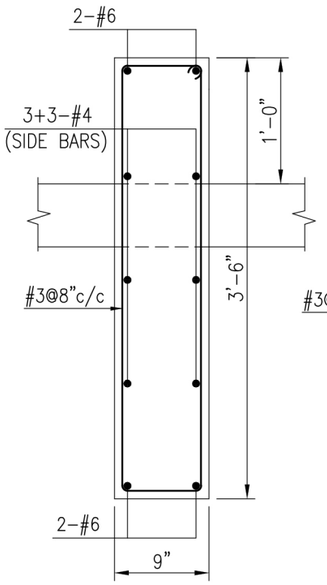

BEAM FB-12A

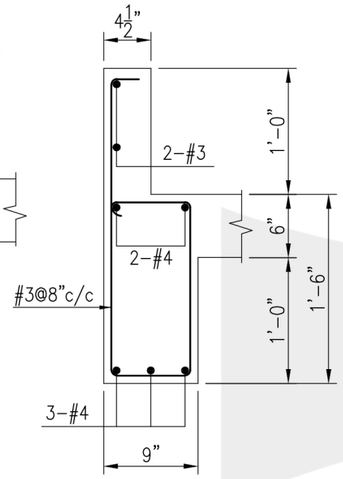

BEAM FB-13

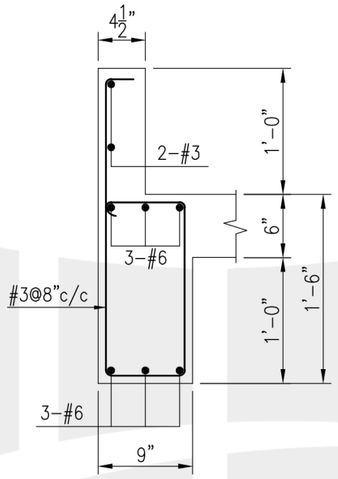

BEAM FB-14

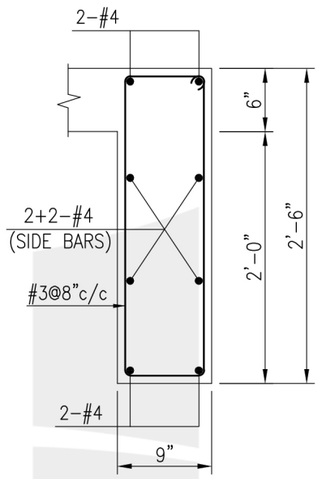

BEAM FB-15

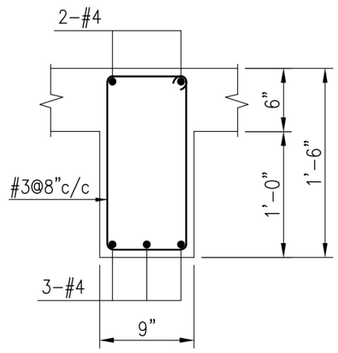

BEAM FB-16

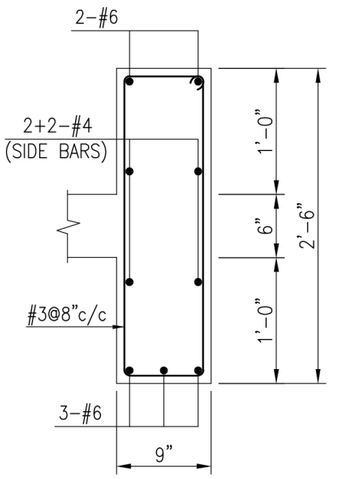

BEAM FB-17

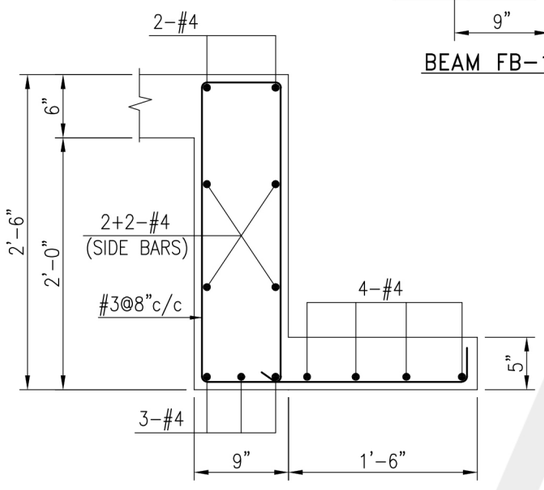

BEAM FB-18

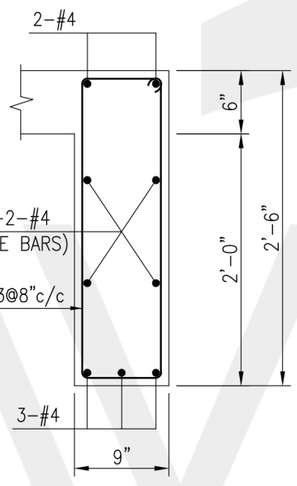

BEAM FB-19

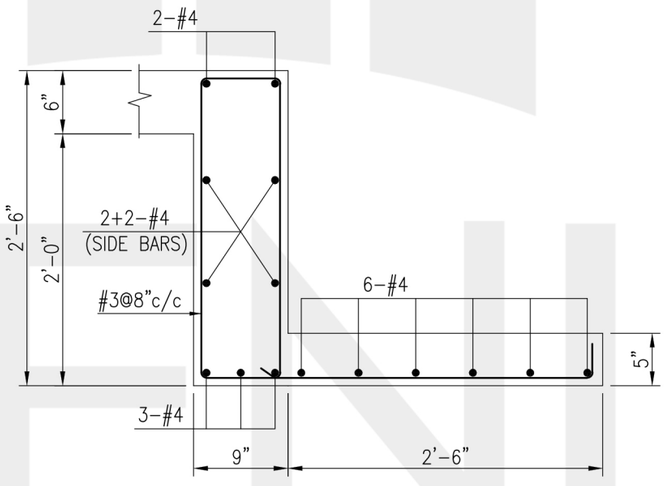

BEAM FB-20

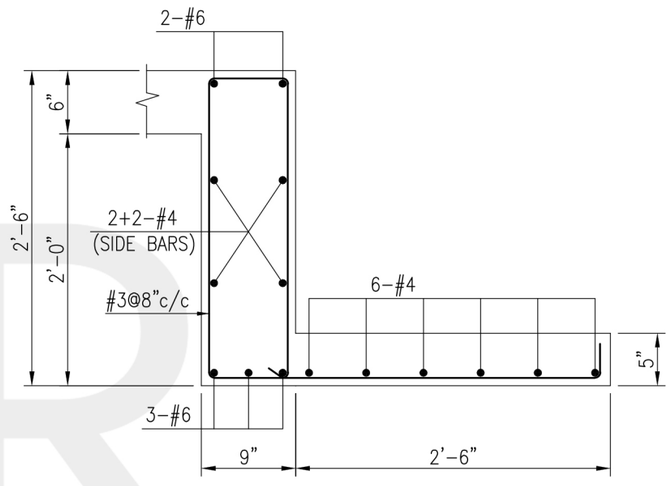

BEAM FB-21

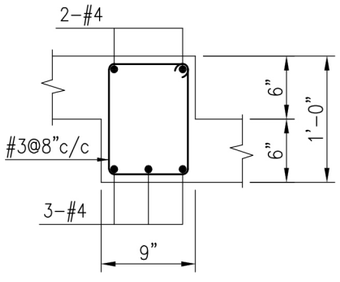

CONCEALED BEAM CB-1

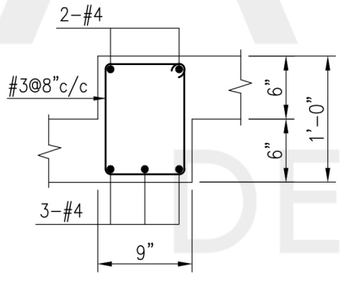

CONCEALED BEAM CB-2
(SECTION 2-2)

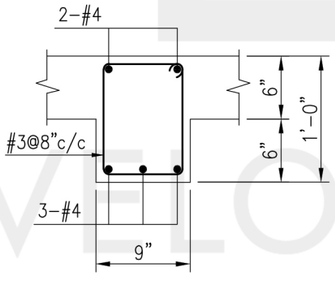

CONCEALED BEAM CB-2
(SECTION 2A-2A)

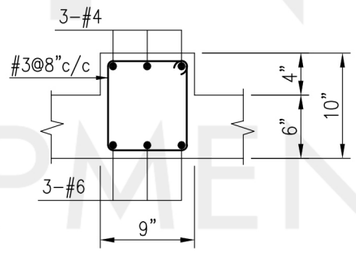

CONCEALED BEAM CB-3

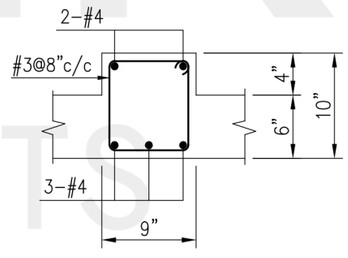

CONCEALED BEAM CB-4

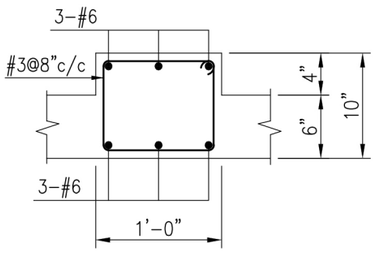

CONCEALED BEAM CB-5

TITLE: BEAMS REINFORCEMENT DETAIL (FIRST FLOOR SLAB) (BEAMS FB-12 TO FB-21 & CB-1 TO CB-5)	PROJECT: PLOT # 588, STREET 8-A, SECTOR M1, LAKE CITY, LAHORE.	DESIGN CONSULTANT:	STRUCTURE CONSULTANT:	DESIGNED BY:		DRAWN BY:	DWG: S-05
				DATE:	26-01-2026		
				REVISION DATE:	00-00-0000	00	
				SCALE:	AS SHOWN		

AVENIR DEVELOPMENTS

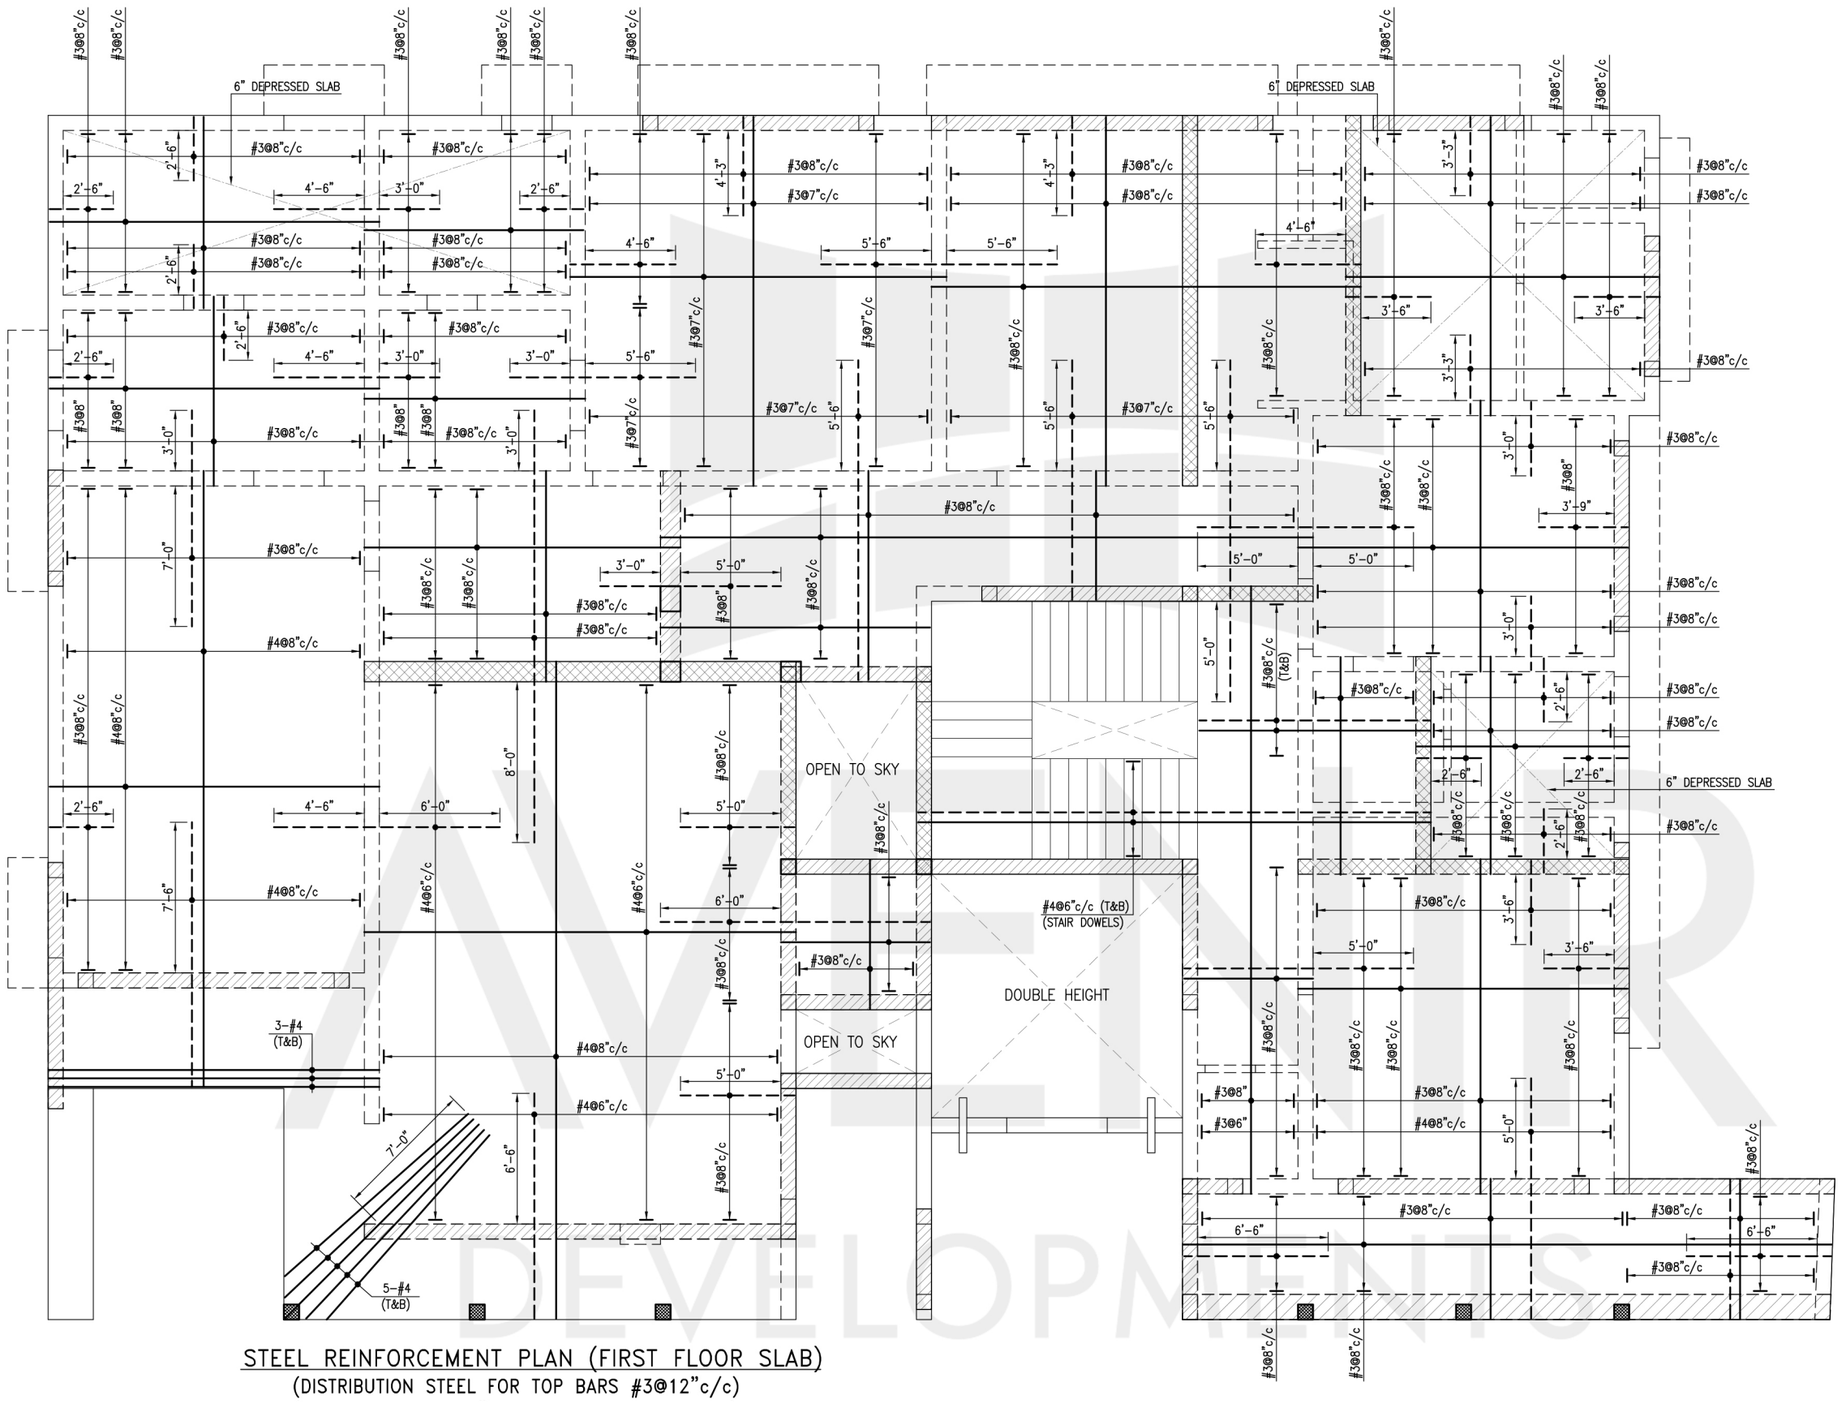

STEEL REINFORCEMENT PLAN (FIRST FLOOR SLAB)

(DISTRIBUTION STEEL FOR TOP BARS #3@12"c/c)

(SLAB THICKNESS =6" UNLESS NOTED OTHERWISE)

TITLE: STEEL REINFORCEMENT PLAN (FIRST FLOOR SLAB)	PROJECT: PLOT # 588, STREET 8-A, SECTOR M1, LAKE CITY, LAHORE.	DESIGN CONSULTANT:	STRUCTURE CONSULTANT:	DESIGNED BY:	DRAWN BY:	DWG: S-06
				DATE:	26-01-2026	
				REVISION DATE:	00-00-0000	00
				SCALE:	AS SHOWN	

AVENUE DEVELOPMENTS

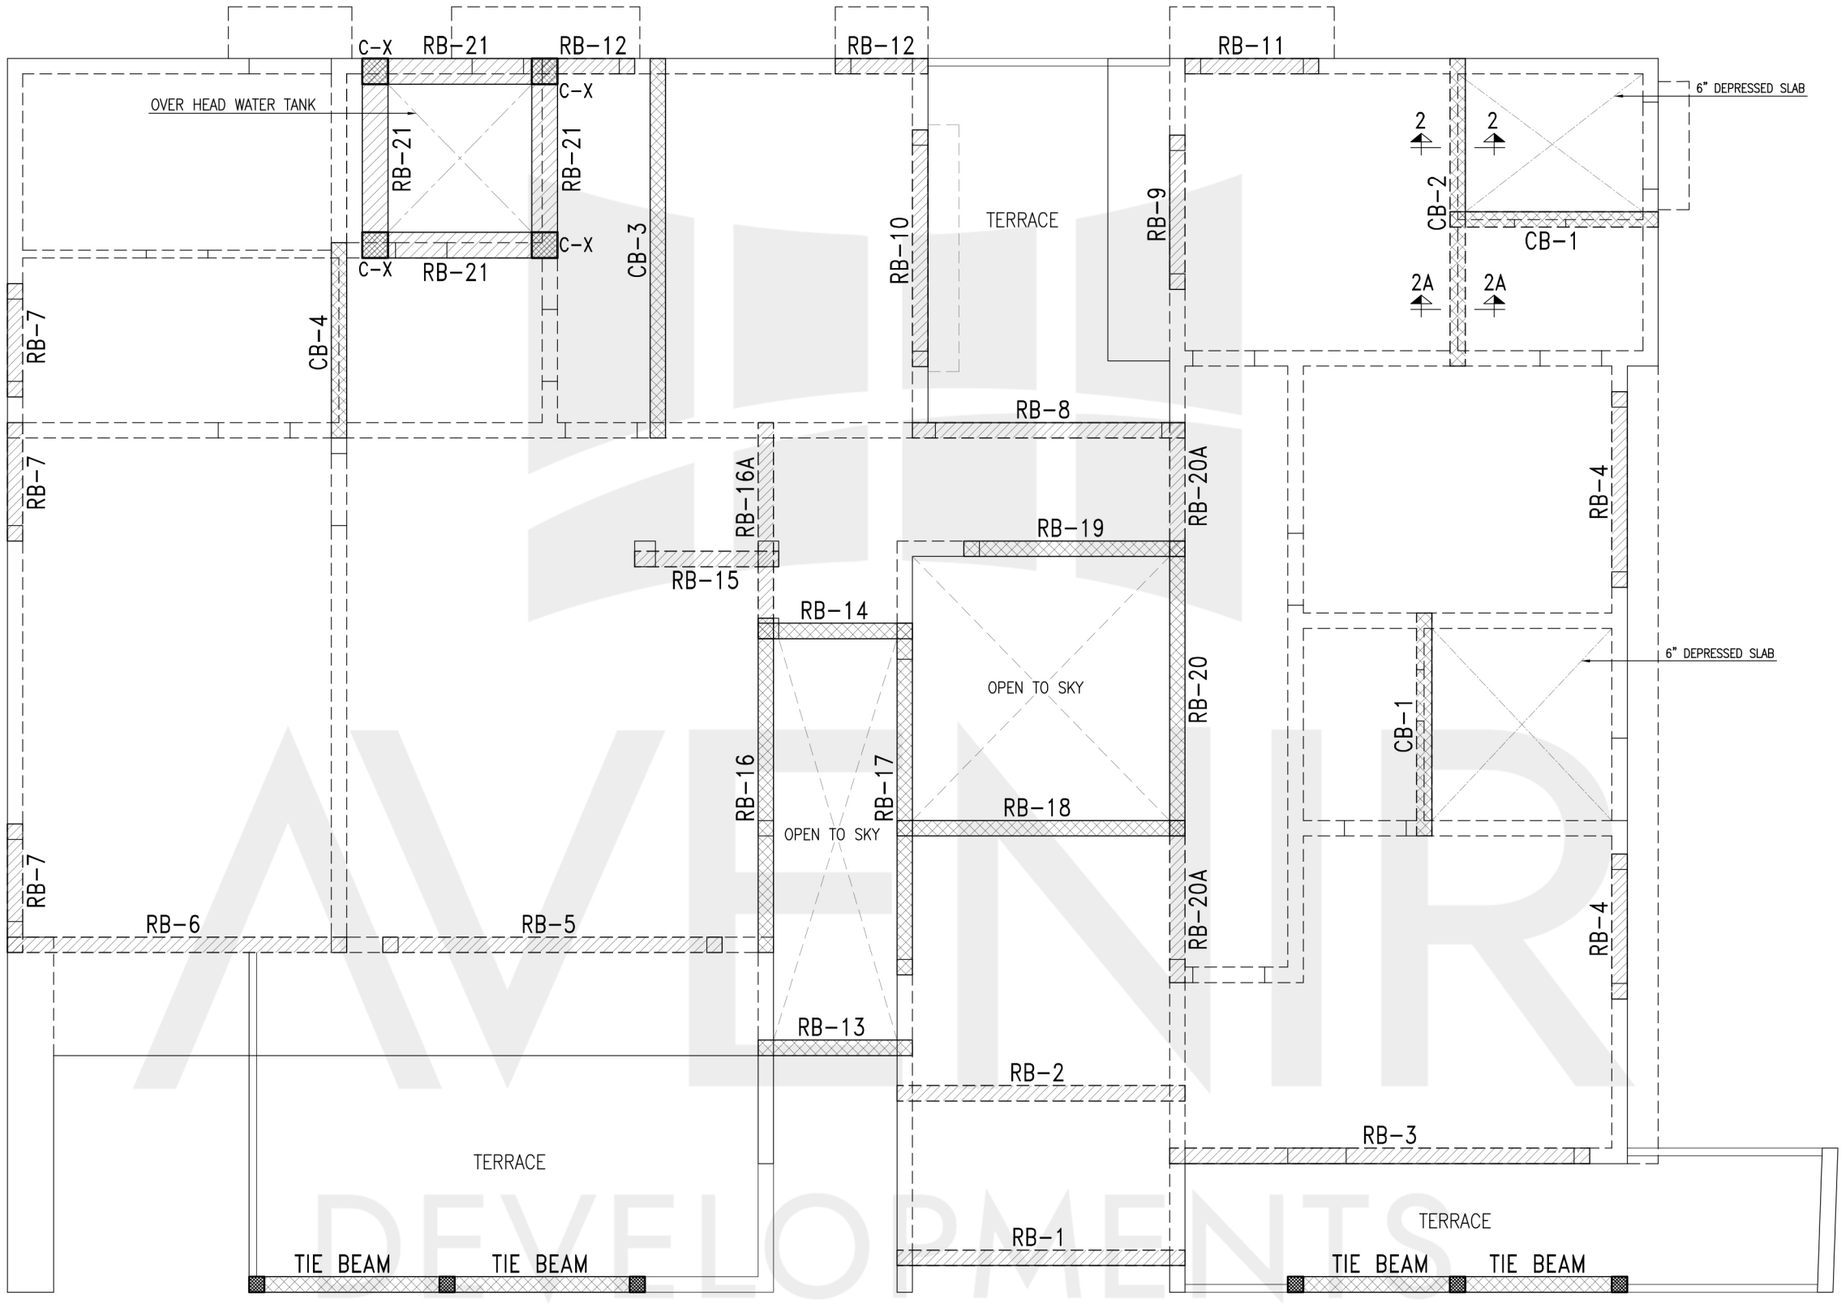

BEAMS FRAMING PLAN (ROOF SLAB)

TITLE: BEAMS FRAMING PLAN (ROOF SLAB)	PROJECT: PLOT # 588, STREET 8-A, SECTOR M1, LAKE CITY, LAHORE.	DESIGN CONSULTANT:	STRUCTURE CONSULTANT:	DESIGNED BY:		DRAWN BY:	DWG: S-07
				DATE:	26-01-2026		
				REVISION DATE:	00-00-0000	00	
				SCALE:	AS SHOWN		

AVENIR DEVELOPMENTS

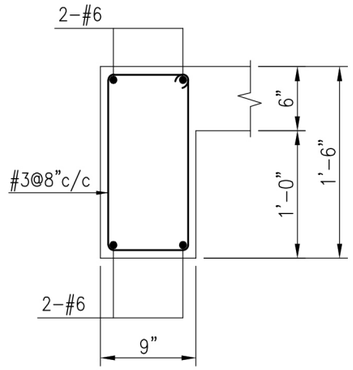

BEAM RB–1

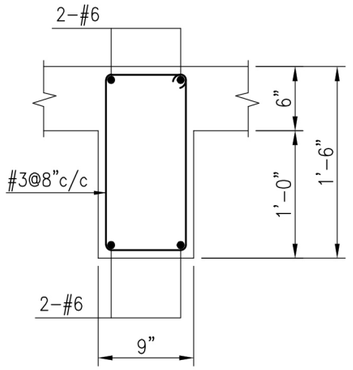

BEAM RB–2

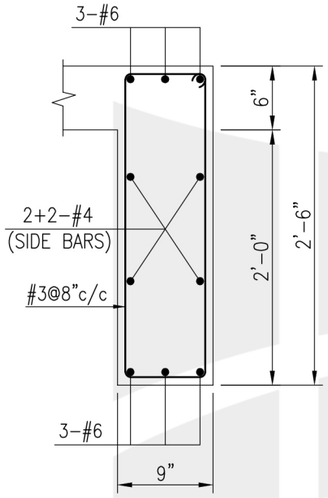

BEAM RB–3

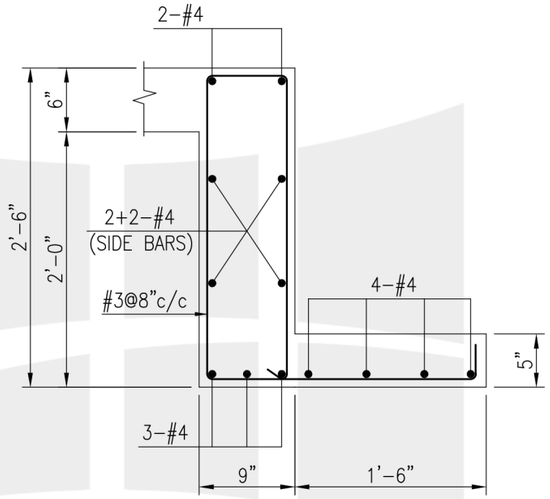

BEAM RB–4

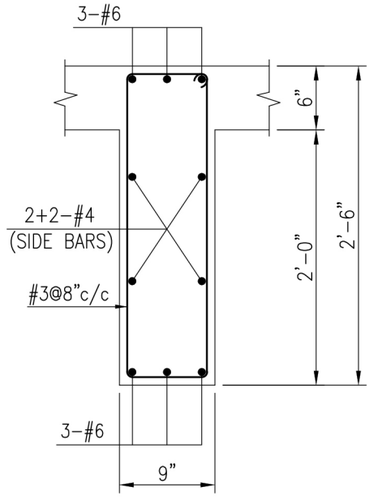

BEAM RB–5

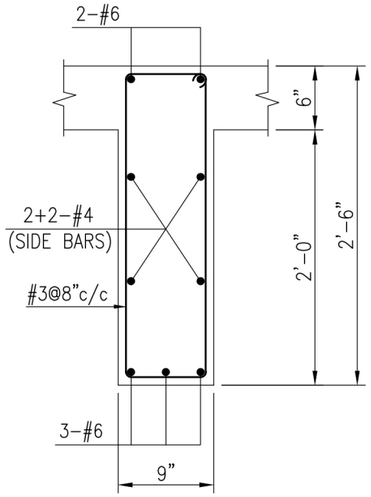

BEAM RB–6

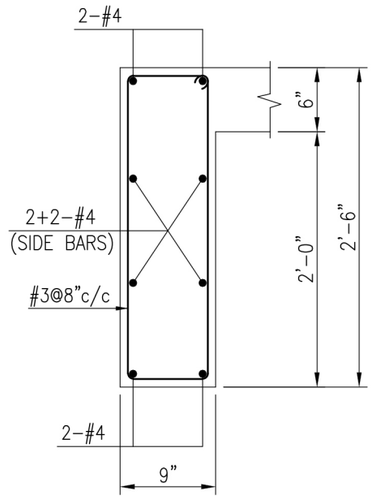

BEAM RB–7

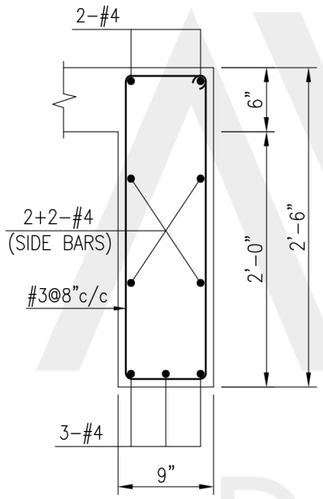

BEAM RB–8

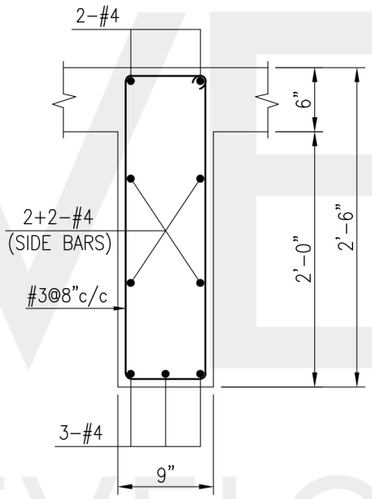

BEAM RB–9

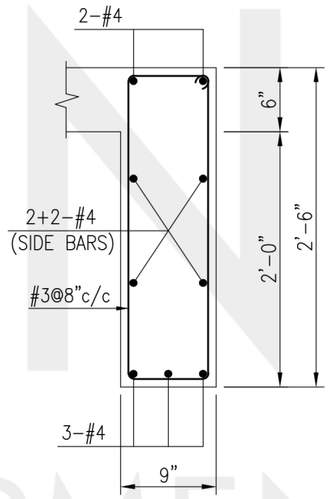

BEAM RB–10

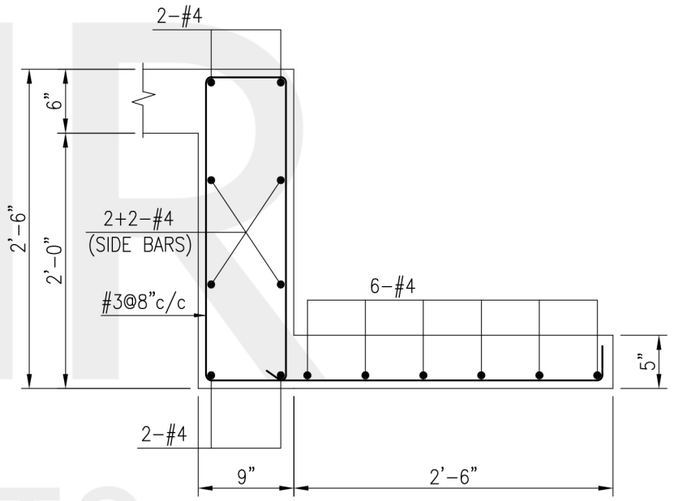

BEAM RB–11 & RB–12

AVENUE DEVELOPMENTS

TITLE: BEAMS REINFORCEMENT DETAIL (ROOF SLAB) (BEAMS RB-1 TO RB-12)	PROJECT: PLOT # 588, STREET 8-A, SECTOR M1, LAKE CITY, LAHORE.	DESIGN CONSULTANT:	STRUCTURE CONSULTANT:	DESIGNED BY:	DRAWN BY:	DWG: S-08
				DATE:	26-01-2026	
				REVISION DATE:	00-00-0000 / 00	
				SCALE:	AS SHOWN	

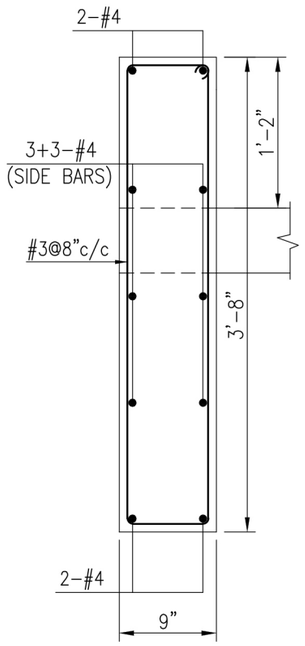

BEAM RB–13

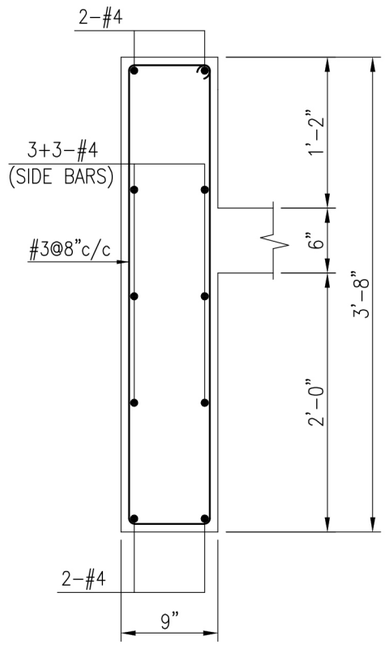

BEAM RB–14

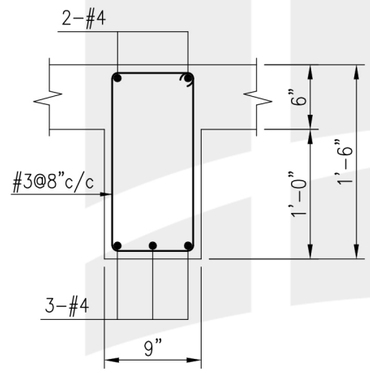

BEAM RB–15

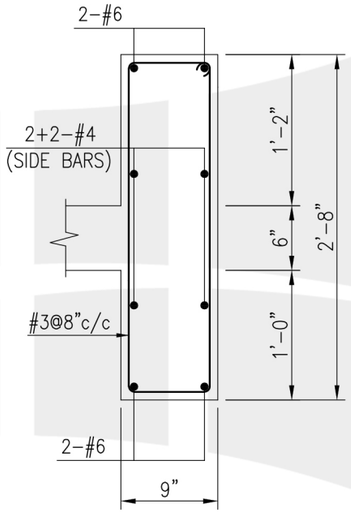

BEAM RB–16

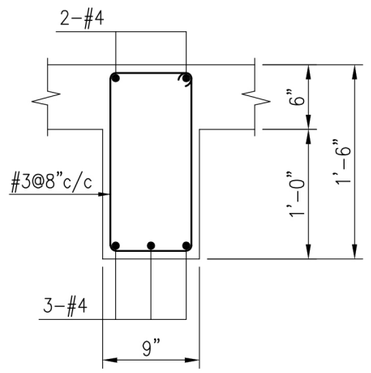

BEAM RB–16A

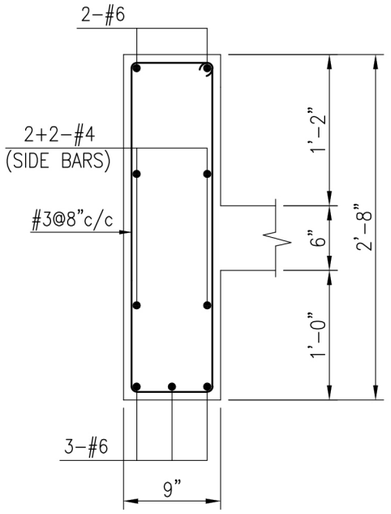

BEAM RB–17

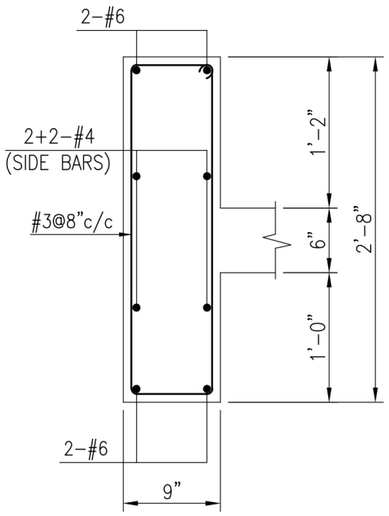

BEAM RB–18

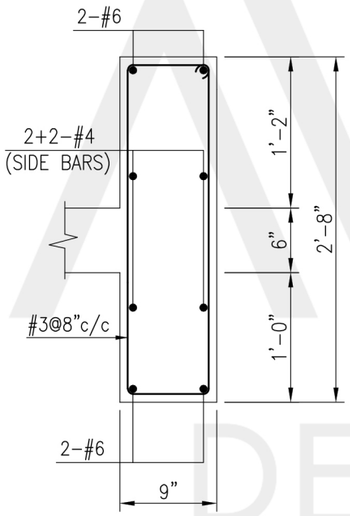

BEAM RB–19

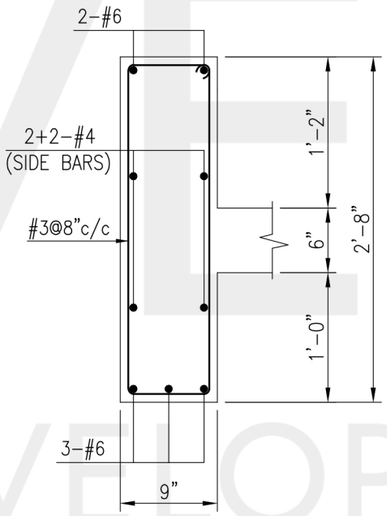

BEAM RB–20

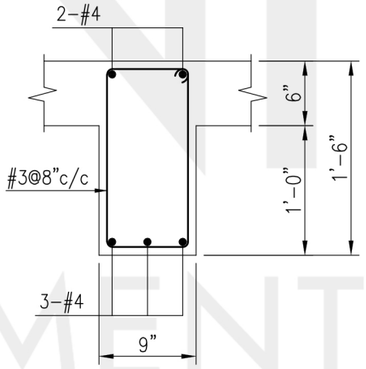

BEAM RB–20A

TITLE: BEAMS REINFORCEMENT DETAIL (ROOF SLAB) (BEAMS RB-13 TO RB-20)	PROJECT: PLOT # 588, STREET 8-A, SECTOR M1, LAKE CITY, LAHORE.	DESIGN CONSULTANT:	STRUCTURE CONSULTANT:	DESIGNED BY:	DRAWN BY:	DWG: S-09
				DATE:	26-01-2026	
				REVISION DATE:	00-00-0000	00
				SCALE:	AS SHOWN	

AVENIR DEVELOPMENTS